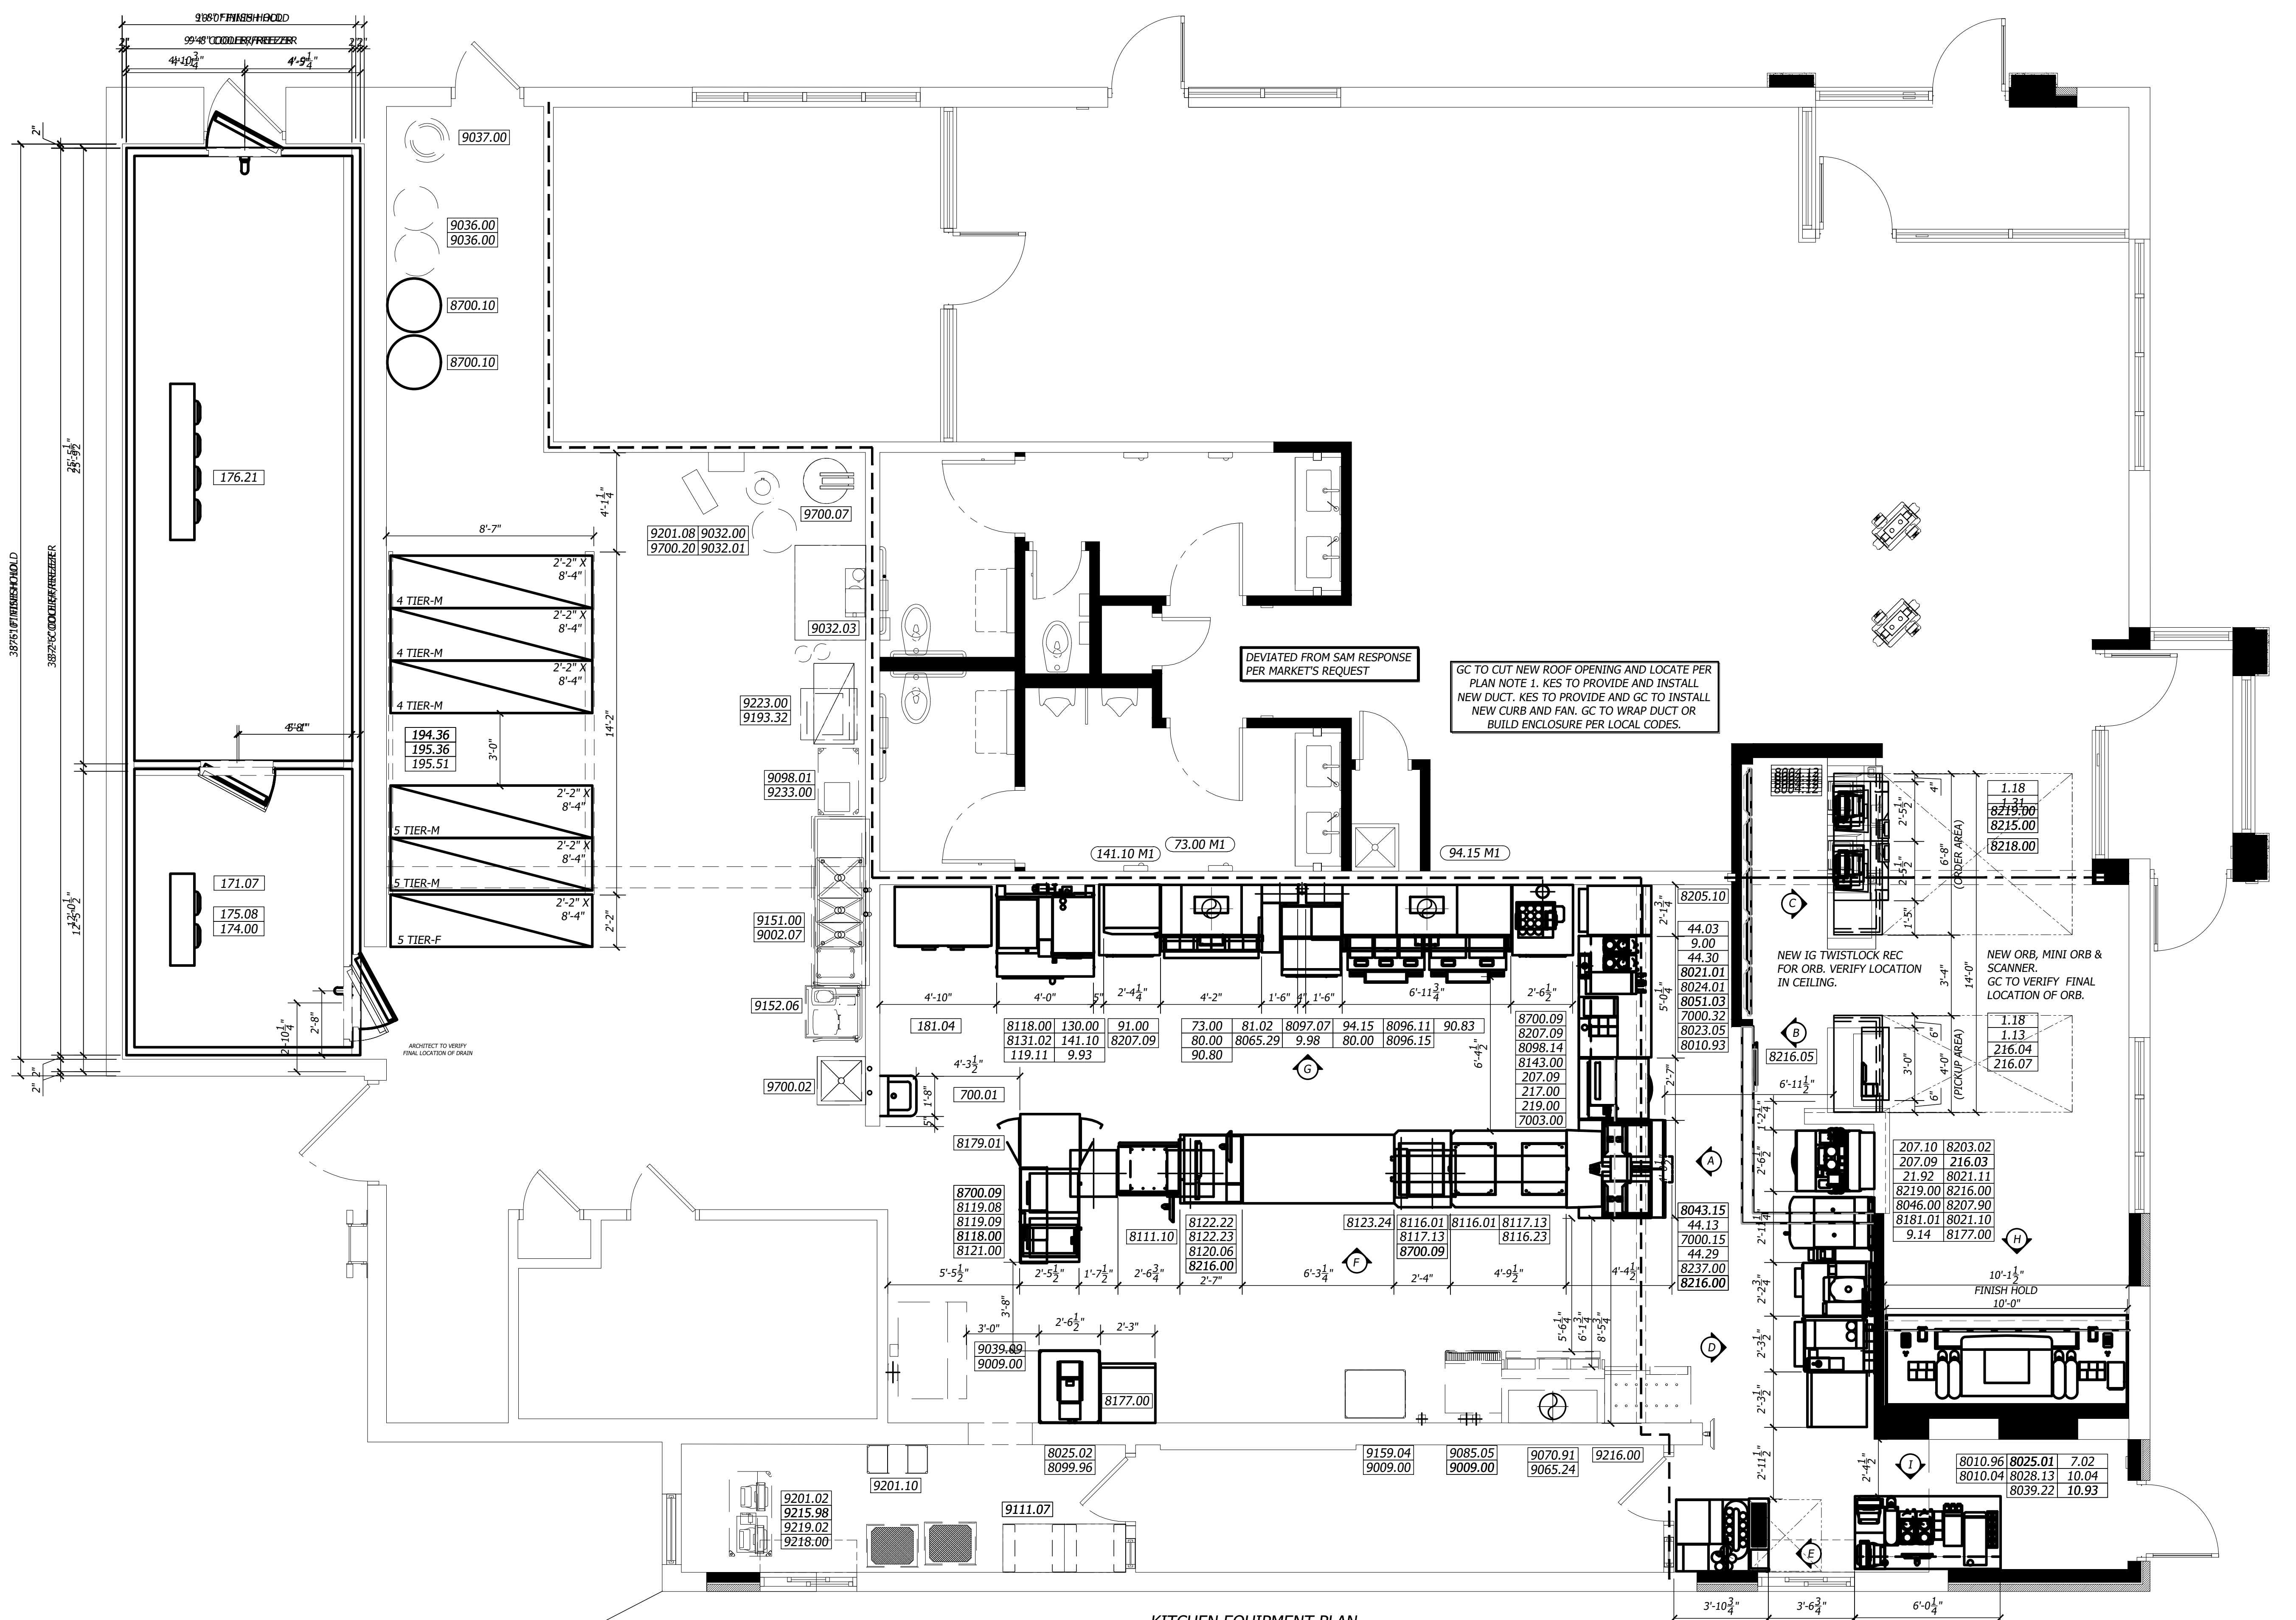
DEVIATED FROM SAM RESPONSE PER MARKET'S REQUEST
GC TO CUT NEW ROOF OPENING AND LOCATE PER PLAN NOTE 1. KES TO PROVIDE AND INSTALL NEW DUCT. KES TO PROVIDE AND GC TO INSTALL NEW CURB AND FAN. GC TO WRAP DUCT OR BUILD ENCLOSURE PER LOCAL CODES.
NEW IG TWISTLOCK REC FOR ORB. VERIFY LOCATION IN CEILING.
NEW ORB, MINI ORB & SCANNER. GC TO VERIFY FINAL LOCATION OF ORB.
(ORDER AREA)
(PICKUP AREA)
FINISH HOLD
4 TIER-M
5 TIER-M
5 TIER-F
73.00 M1
94.15 M1
141.10 M1
A
B
C
D
E
F
G
H
I
J

KITCHEN EQUIPMENT PLAN

PROVIDE IF REQUIRED

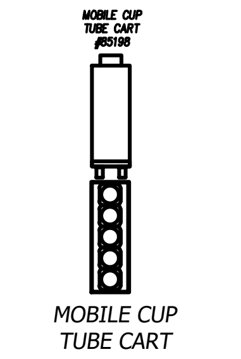

MOBILE CUP TUBE CART

45.47

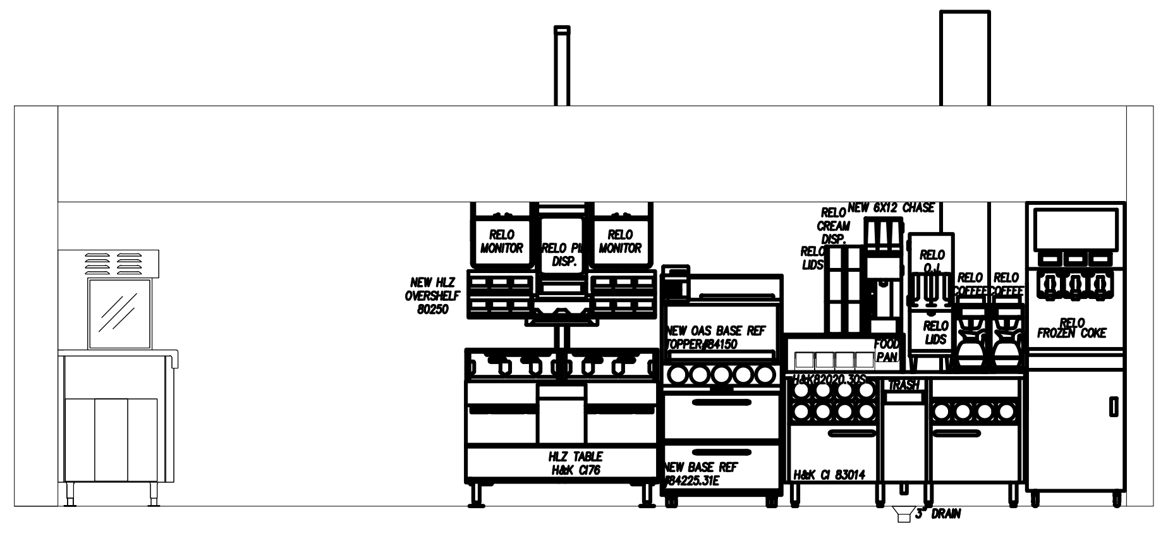

A CENTER ISLAND ELEVATION

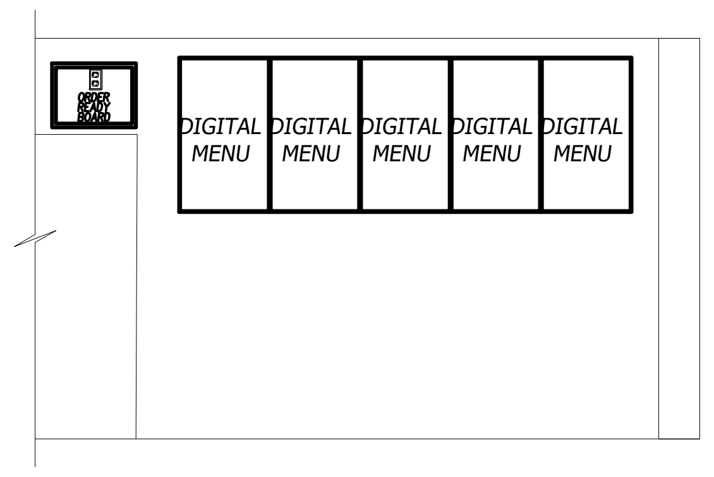

B S.A.M. WALL ELEVATION

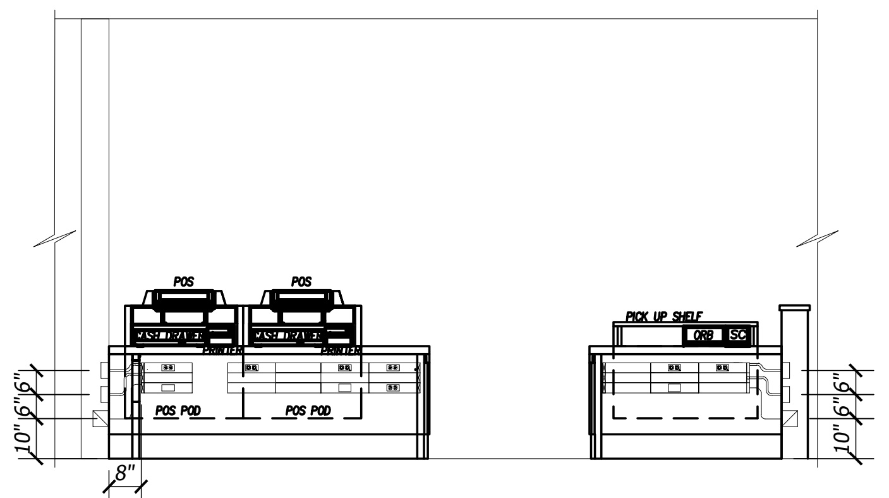

C FRONT COUNTER ELEVATION

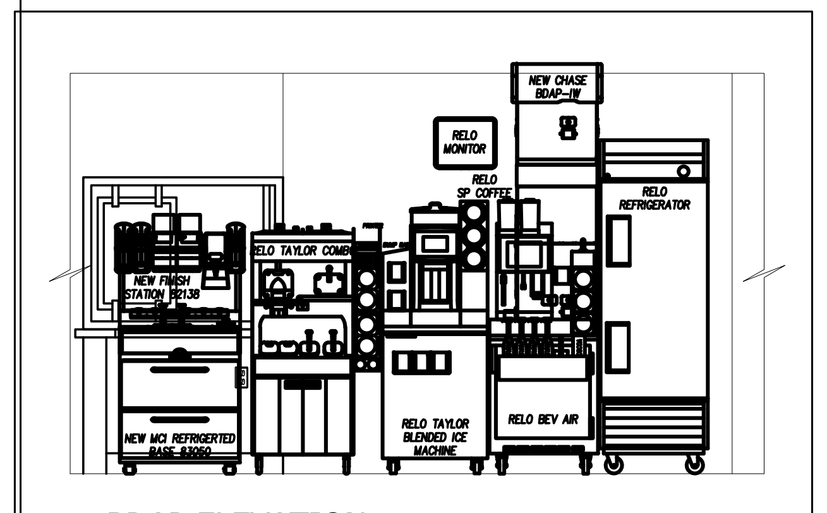

D BDAP ELEVATION

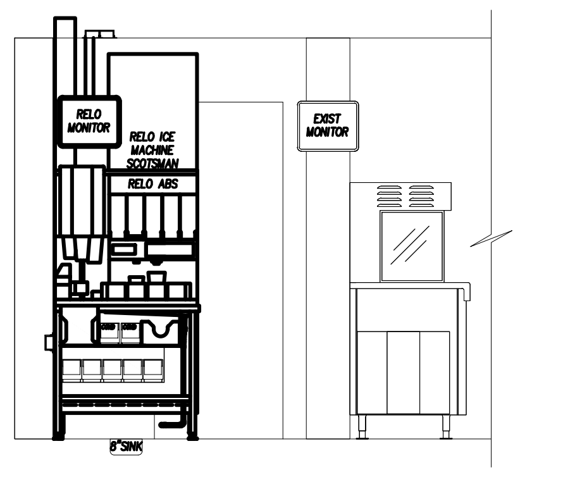

E DRIVE THRU ELEVATION

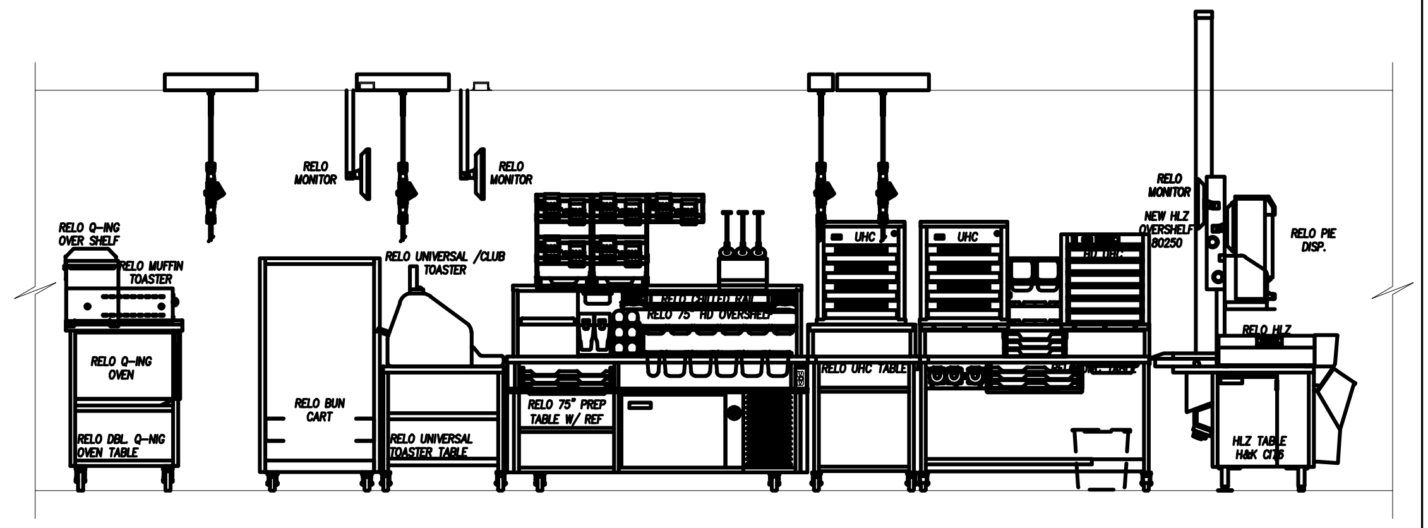

F PREP LINE ELEVATION

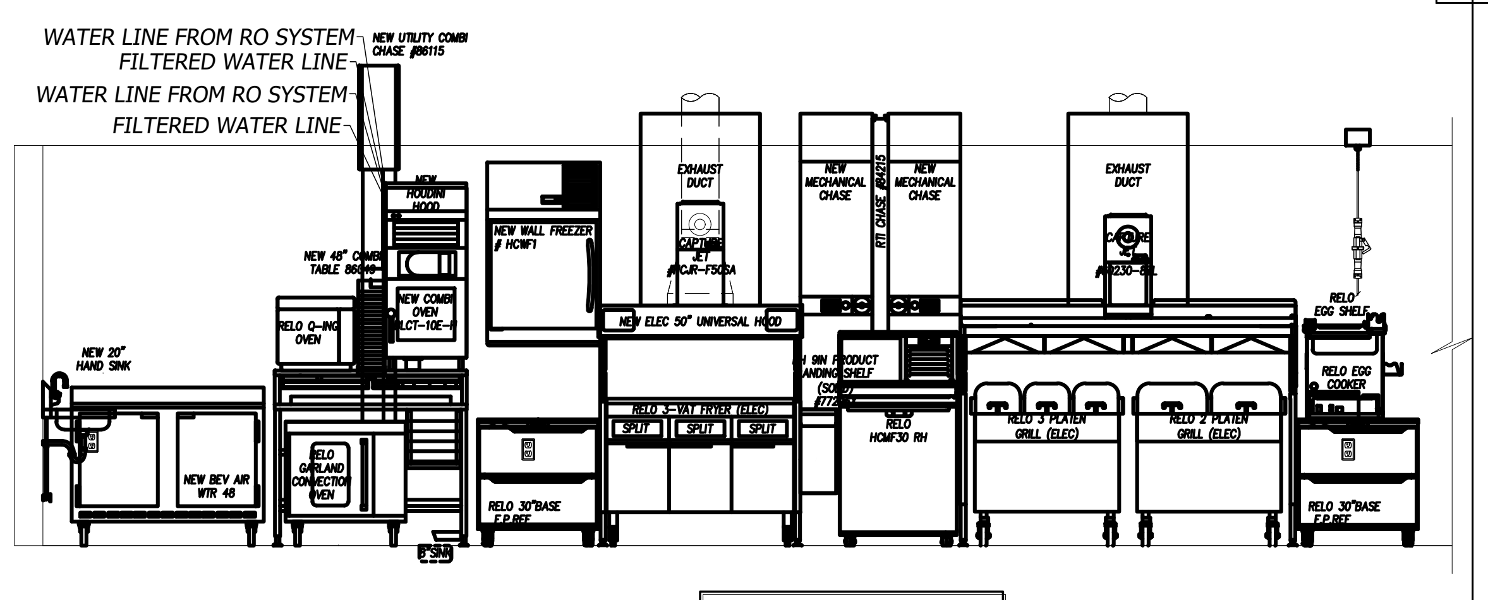
WATER LINE FROM RO SYSTEM- FILTERED WATER LINE
WATER LINE FROM RO SYSTEM- FILTERED WATER LINE

NEW CASTERS FOR RELOCATED CONVECTION OVEN ARE REQUIRED

G GRILL LINE ELEVATION

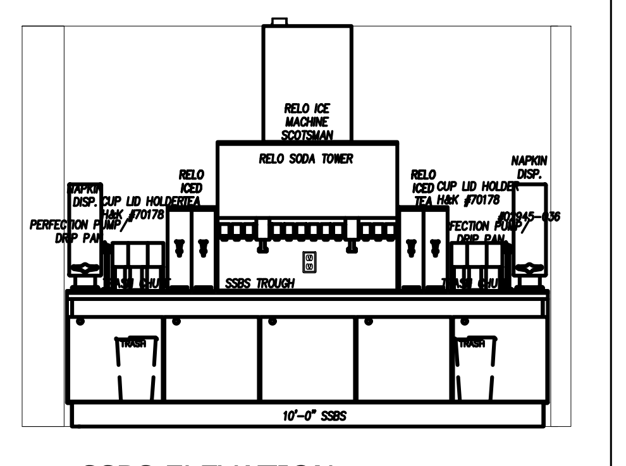

H SSBS ELEVATION

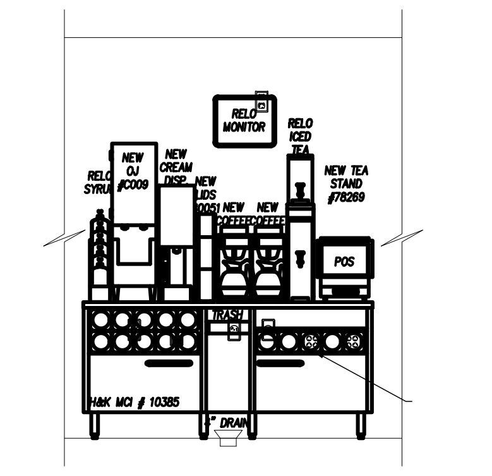

I DRIVE THRU ELEVATION

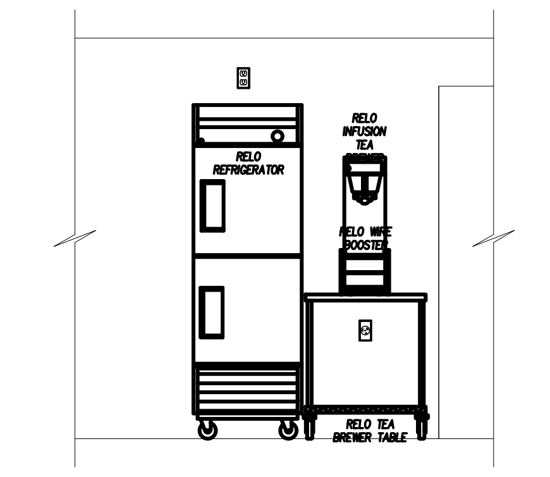

J TEA BREWER ELEVATION

GENERAL NOTES

1) USE EXISTING ROOF OPENINGS UNLESS OTHERWISE NOTED ON SCOPE OF WORK. IF NEW EXHAUST FAN ROOF OPENING IS REQUIRED, GC TO VERIFY PROPOSED ROOF OPENING LOCATION IS LOCATED A MIN. OF 10'-0" FROM HVAC AIR INTAKE. GC TO CUT NEW ROOF OPENING AND INSTALL NEW CURB AND FAN. H&K INSTALLER TO INSTALL NEW DUCT. GC TO WRAP DUCT OR CONSTRUCT ENCLOSURE IF REQUIRED BY LOCAL CODES. EC TO WIRE EXHAUST FAN TO ANSUL INTERLOCK SYSTEM.

2) KITCHEN INSTALLER TO MOUNT RACEWAY BELOW HOOD. EC TO MAKE FINAL CONNECTIONS FROM RACEWAY TO TERMINAL BLOCK INSIDE CHASE. IF GAS, KITCHEN INSTALLER TO WALL MOUNT GAS MANIFOLD BELOW HOOD. PC TO INSTALL QUICK DISCONNECT LINES AND MAKE FINAL CONNECTIONS TO IN-BOUND GAS LINE FROM CHASE AND TO INDIVIDUAL APPLIANCES.

3) ALL UTILITIES FOR APPLIANCES BELOW HOOD TO RUN OVERHEAD AND DOWN MECHANICAL CHASE. EC TO MAKE FINAL CONNECTIONS TO TERMINAL BLOCK INSIDE CHASE. IF GAS, PC TO MAKE FINAL CONNECTIONS AT GAS MANIFOLD.

4) IF CHASE IS RELOCATED, GC TO COORDINATE MODIFICATION OF ANSUL SYSTEM WITH ANSUL. RELOCATE OR PROVIDE NEW UTILITIES AS NEEDED.

5) GC TO VERIFY ALL EXISTING UTILITIES AND STRUCTURAL FLOOR LOADING CONDITIONS. REMOVE, CLOSE, SEAL, CAP AND/OR RELOCATE EXISTING LINES, DRAINS & UTILITIES. RUN DRAIN LINES TO EXISTING FLOOR DRAINS IF POSSIBLE, OR RELOCATE/INSTALL NEW FLOOR DRAINS, GAS LINES, AND SLEEVES AS NEEDED. THE GC SHALL COORDINATE ALL FINAL CONNECTIONS TO EQUIPMENT WHERE APPLICABLE.

6) GC TO REMOVE, CLOSE, SEAL, CAP, RELOCATE, OR INSTALL NEW LINES, DRAINS, RECEPTACLES, CORDS, UTILITIES, ROOF OPENINGS AS NEEDED FOR NEW AND RELOCATED EQUIPMENT. GC TO PATCH, SEAL AND/OR FINISH WALL, FLOOR, CEILING AND/OR ROOF AS NECESSARY TO MATCH EXISTING.

7) GC AND INSTALLER TO VERIFY LOCATION OF EXISTING EQUIPMENT TO REMAIN IN RELATION TO NEW AND RELOCATED EQUIPMENT.

8) REMOVE AND REPLACE DAMAGED QUARRY TILE FLOORING ADJACENT TO THE PROJECT AREA(S). MATCH EXISTING QUARRY TILE WHERE PATCHING DAMAGED TILE OR WHERE EXTENDING THE TILE FIELD IN NEW FLOOR AREAS.

9) IN THE EVENT REMOVAL OR RELOCATION OF EQUIPMENT RESULTS IN EXPOSING EXISTING KITCHEN FLOOR TILE THAT IS NOT ABRASIVE, GC SHALL REPLACE ALL EXISTING SMOOTH KITCHEN QUARRY TILE WITH ABRASIVE QUARRY TILE. SUCH REPLACEMENT TILE SHALL BE LOCATED, AT A MINIMUM, IN FRONT OF ALL GRILLS, FRYERS, BAGGING STATIONS, SINKS OR ANY LOCATION WHERE GREASE OR WATER CAN ACCUMULATE ON THE FLOOR CAUSING A SLIP AND FALL HAZARD. THE TILE SHALL EXTEND A MINIMUM OF ONE TILE COURSE UNDER THE EDGE OF THE FIXTURE OR EQUIPMENT AND EXTEND THE ENTIRE LENGTH OF THE FIXTURE OR EQUIPMENT.

10) INSTALLER TO INSTALL NEW AND RELOCATED EQUIPMENT, GC TO MAKE FINAL CONNECTIONS.

11) ALL INTERIOR FINISHES SHALL BE COORDINATED WITH DECOR & SEATING DRAWINGS BY OTHERS.

12) GC TO OBTAIN ALL PERMITS REQUIRED PER LOCAL CODE.

13) ALL WORK SHALL COMPLY WITH ALL APPLICABLE STATE AND LOCAL HEALTH, SAFETY AND CONSTRUCTION CODES. G.C., E.C., P.C. TO VERIFY THAT ALL KITCHEN EQUIPMENT, SAFETY AND INTERLOCK UTILITIES ARE FUNCTIONAL AND IN CONFORMANCE WITH ALL LOCAL CODES PRIOR TO COMPLETION OF REMODEL. G.C. TO COORDINATE ANY CORRECTIONS OF ANY DEFICIENCIES WITH McDONALD'S CONSTRUCTION, SUBCONTRACTORS, AND/OR OWNER/OPERATOR.

14) ALL ELECTRICAL MATERIAL USED ON THIS PROJECT SHALL BE "UL" LISTED AND LABELED.

15) ALL DIMENSIONS SHOWN ARE TAKEN FROM FACE OF WALL FINISH. THE GC/ALL TRADES SHALL MAKE NECESSARY DIMENSIONAL ALLOWANCES.

16) ALL J-BOXES, DCO'S, AND OTHER ELECTRICAL DEVICES SHOWN SHALL BE RECESSED MOUNTED INTO A WALL, FLOOR OR CEILING UNLESS SPECIFICALLY NOTED OTHERWISE.

17) ALL RECEPTACLES (EXCEPT SPECIFIED HUBBLE PIN AND SLEEVE) SHALL BE FURNISHED BY THE E.C. THE RECEPTACLES INCLUDING PIN AND SLEEVE TYPE SHALL BE INSTALLED BY THE EC.

18) EC SHALL PROVIDE AND INSTALL STAINLESS COVER PLATES ON ALL RECEPTACLES AND J-BOXES. ADDITIONALLY, EC SHALL PROVIDE AND INSTALL ORANGE NYLON COVER PLATES MARKED "COMPUTER ONLY" ON ALL ISOLATED GROUND/DEDICATED RECEPTACLES.

19) POWER AND CONTROL CORDS ARE FURNISHED WITH KITCHEN APPLIANCES. THE EC SHALL CONNECT CORD SETS TO APPLIANCES AS REQUIRED.

20) MOST KITCHEN REMODELS WILL REQUIRE SOME LEVEL OF CEILING REPAIR. THIS WILL BE THE RESPONIBILITY OF THE GC.

21) ALL HOLES IN FRONT COUNTER FOR POS CORDS AND CABLES SHALL BE LOCATED BY OWNER AND DRILLED BY GC.

22) EC SHALL PROVIDE A DUPLEX RECEPTACLE AND LOW VOLTAGE BROADBAND CONNECTION FOR THE INSTALLATION OF PLASMA TELEVISIONS. COORDINATE EXACT LOCATIONS WITH PM & DECOR COMPANY. FOR BROADBAND CONNECTION, EC SHALL PROVIDE A 4 X 4 BOX WITH A 3/4" CONDUIT STUB-UP WITH A BUSHING INTO ACCESSIBLE CEILING SPACE.

23) WHERE PIPING IS LOCATED WITHIN WALL CAVITIES, ACCESS TO THE CLEANOUTS SHALL BE PROVIDED.

24) DIMENSIONS SHOWING THE LOCATION OF DRAINS AND FLOOR SINKS ARE CENTERLINE DIMENSIONS.

25) GAS PIPING SHALL NOT PENETRATE ANY FIRE-RATED CHASE, SHAFT, DUCTWORK OR PLENUM.

26) GC TO RE-BALANCE THE HVAC SYSTEM AFTER ANY EXHAUST HOOD HAS BEEN REPLACED OR RELOCATED.

27) ALL EQUIPMENT SHALL BE INSTALLED IN ACCORDANCE WITH ITS LISTING AND/OR THE MANUFACTURER'S INSTALLATION INSTRUCTIONS.

28) UPON COMPLETION OF INSTALLATION, THE GAS PIPING SYSTEM SHALL BE PURGED OF DELETERIOUS MATERIAL AND SHALL BE PRESSURE TESTED. IF THE MINIMUM PRESSURES ARE NOT MET, THIS SHALL BE IMMEDIATELY REPORTED TO THE MCDONALD'S CONSTRUCTION MANAGER.

29) FLEXIBLE DUCTWORK SHALL NOT PENETRATE WALLS. SHEET METAL DUCTWORK IS REQUIRED AT ALL FIRE-RATED AND DRAFT STOP WALL PENETRATIONS.

30) ALL GREASE EXHAUST DUCTWORK SEAMS AND JOINTS SHALL BE CONTINUOUSLY WELDED WATER-TIGHT ON THE EXTERNAL SURFACE OF THE DUCT SYSTEM. ALL WELDING SHALL BE PERFORMED BY A CERTIFIED WELDER.

31) IN THE EVENT OF ADDITIONAL FRYER CAPACITY, THE O/O MUST ENGAGE LICENSED MECHANICAL ENGINEER. THE M/E WILL BE REQUIRED TO ASSESS THE EXISTING EXHAUST HOOD FAN TO ENSURE IT IS CAPABLE OF HIGHER AIRFLOW AT A POTENTIALLY HIGHER STATIC PRESSURE. CONSTRUCTION DRAWINGS WILL BE REQUIRED OF THE M/E FOR PERMITTING. AFTER INSTALLATION, A CERTIFIED TEST AND BALANCE COMPANY WILL BE REQUIRED TO AIR BALANCE THE NEW AND ANY AFFECTED ROOF-TOP HVAC EQUIPMENT DEEMED AS PART OF THE SCOPE OF WORK BY THE M/E.

32) ALL ROOF-TOP CONDENSING UNITS THAT DISCHARGE HORIZONTALLY SHALL BE ORIENTED SUCH THAT THE DISCHARGE DOES NOT BLOW IN THE DIRECTION OF AN OUTDOOR AIR INTAKE.

33) POS INSTALLER TO COORDINATE RELOCATION OF POS SYSTEM WITH O/O AND MCDONALDS CONSTRUCTION. ALL CABLES FURNISHED AND INSTALLED BY POS SUPPLIER.

34) NEW POS(S) ARE SHOWN TO MEET NATIONAL BUILDING AND EQUIPMENT STANDARDS PER MCDONALD'S . FINAL LOCATION OF NEW POS(S) TO BE COORDINATED WITH O/O. POS INSTALLER TO COORDINATE LOCATION OF POS SYSTEM WITH O/O AND MCDONALDS CONSTRUCTION. ALL CABLES FURNISHED AND INSTALLED BY POS SUPPLIER.

35) PLUMBING FOR COMBI OVENS TO BE ROUTED TO FLOOR SINK DRAIN. GC TO VERIFY IF SINK HAS A GREASE INTERCEPT.

SYMBOL LEGEND

⏀	DUPLEX OUTLET (SB OR TL)	─	OPTIONAL EQUIPMENT
⏀	SINGLE OUTLET (SB OR TL)	━	NEW EQUIPMENT ON EQUIPMENT PLAN
⏀	QUAD OUTLET (SB OR TL)	━	RELOCATED EQUIPMENT ON EQUIPMENT PLAN
△	SPECIAL OUTLET (SEE SCHEDULE)	- - -	EXISTING EQUIPMENT
Ⓙ	J-BOX	─	EQUIPMENT ON ROUGH-IN PLAN
▣	DATA CABLE	— — —	EXISTING TRUSSES
○	EXHAUST DUCT ABOVE HOOD	─	SERVICE AREA
○	EXHAUST DUCT ABOVE HOOD	━ ━ ━	NEW MENU BOARD VALANCE
◎	SLEEVE	■	EXISTING FULL WALL
○	REFRIGERATION LINES	─	EXISTING LOW WALL
○	WATER OR GAS LINE	▩	NEW FULL WALL
○	CLEAN OUT	▨	NEW LOW WALL
▤	FLOOR SINK		
⊠	FLOOR DRAIN		

REV	DATE	DESCRIPTION	BY

ENGINEER OF RECORD:

JOHN DALE FERGUSON
4/12/19

PREPARED BY:

CORE STATES
GROUP
CORESTATES, INC.

1700 Industrial Drive
Suite B
Rogers, AR 72756
479.986.4400
www.core-eng.com

PREPARED FOR:

McDonald's USA, LLC

These drawings and specifications are the confidential and proprietary property of McDonald's USA, LLC and shall not be copied or reproduced without written authorization. The contract documents were prepared for use on this specific site in conjunction with its issue date and are not suitable for use on a different site or at a later time. Use of these drawings for reference or example on another project requires the services of properly licensed architects and engineers. Reproduction of the contract documents for reuse on another project is not authorized.

DRAWN BY
CHR

STD ISSUE DATE
MAY 2018

REVIEWED BY
J.FERGUSON

DATE ISSUED
10/12/18

C.S.G. PROJECT #
MCD-24772

TITLE
MRP PROGRAM
CORE 16 2.0

DESCRIPTION
EXISTING MASONRY WALL CONSTRUCTION
EXISTING WOOD ROOF TRUSSES
TILE ARCADES - FRONT, ENTRY

SITE ID
024-0294

SITE ADDRESS
815 EASTLAND DRIVE
JEFFERSON CITY, MO 65101

SHEET NO.
K1.0
KES PLAN

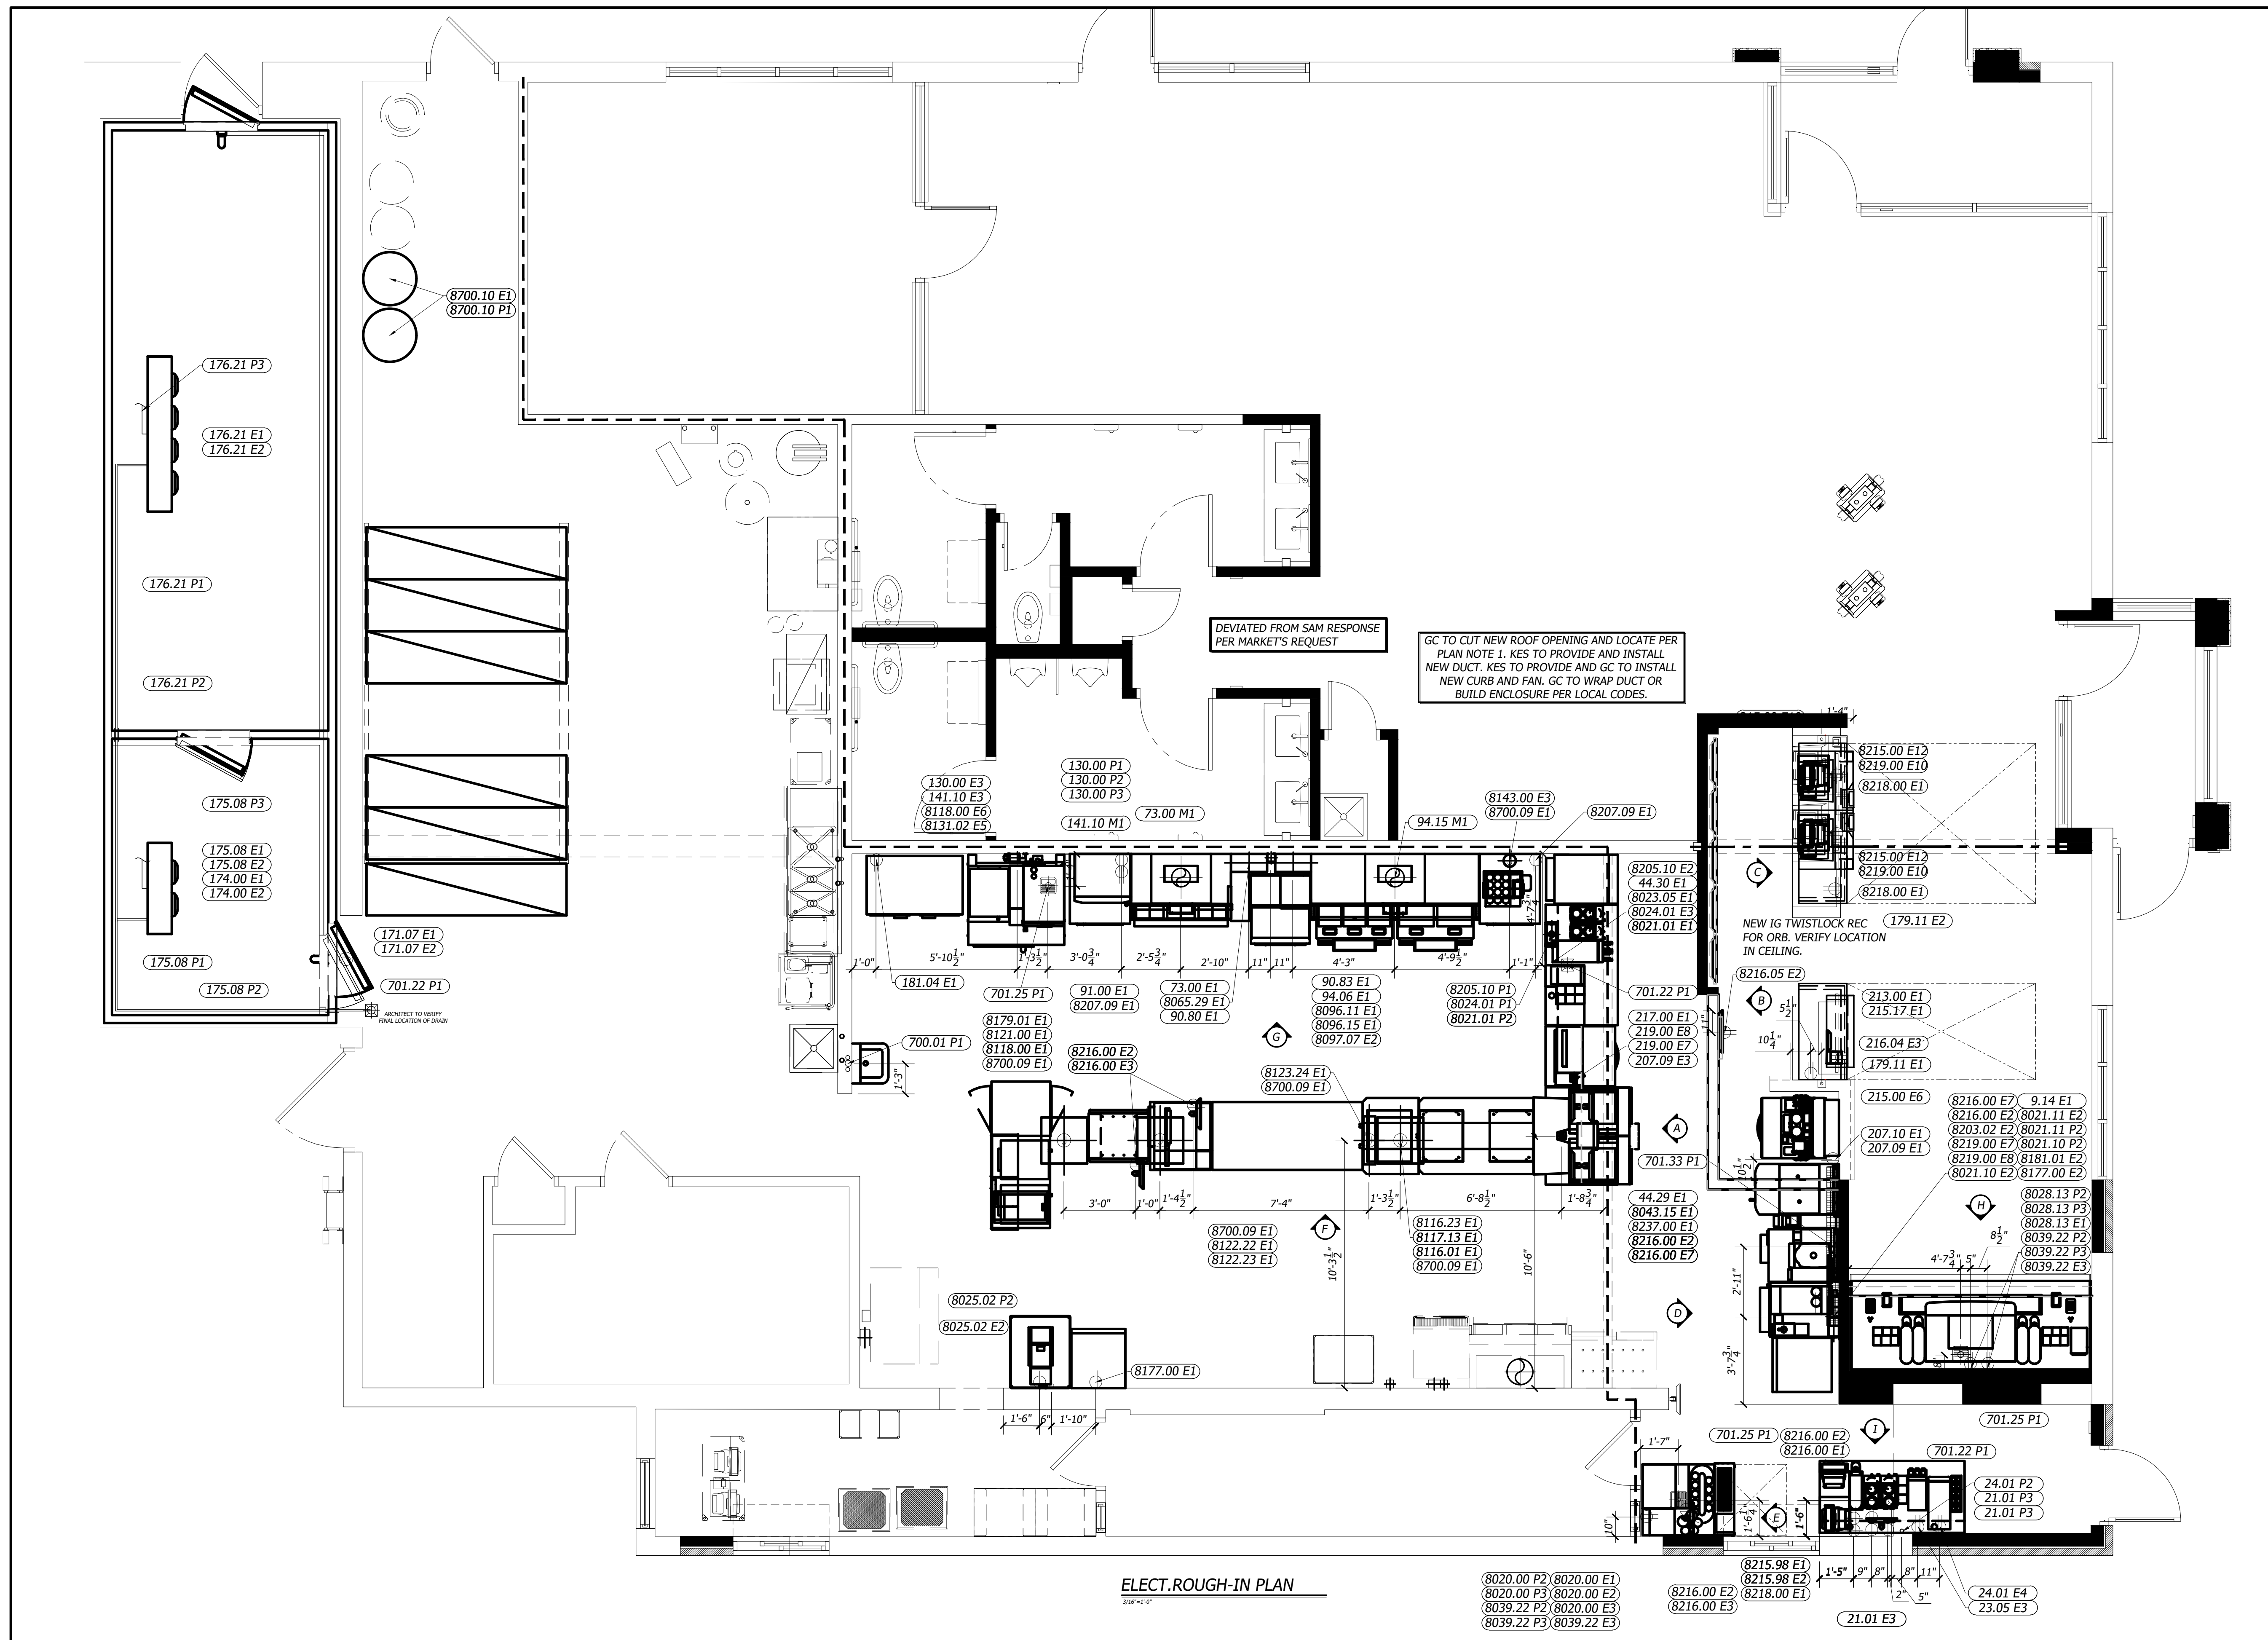
DEVIATED FROM SAM RESPONSE PER MARKET'S REQUEST
GC TO CUT NEW ROOF OPENING AND LOCATE PER PLAN NOTE 1. KES TO PROVIDE AND INSTALL NEW DUCT. KES TO PROVIDE AND GC TO INSTALL NEW CURB AND FAN. GC TO WRAP DUCT OR BUILD ENCLOSURE PER LOCAL CODES.
NEW IG TWISTLOCK REC FOR ORB. VERIFY LOCATION IN CEILING.

ELECT.ROUGH-IN PLAN

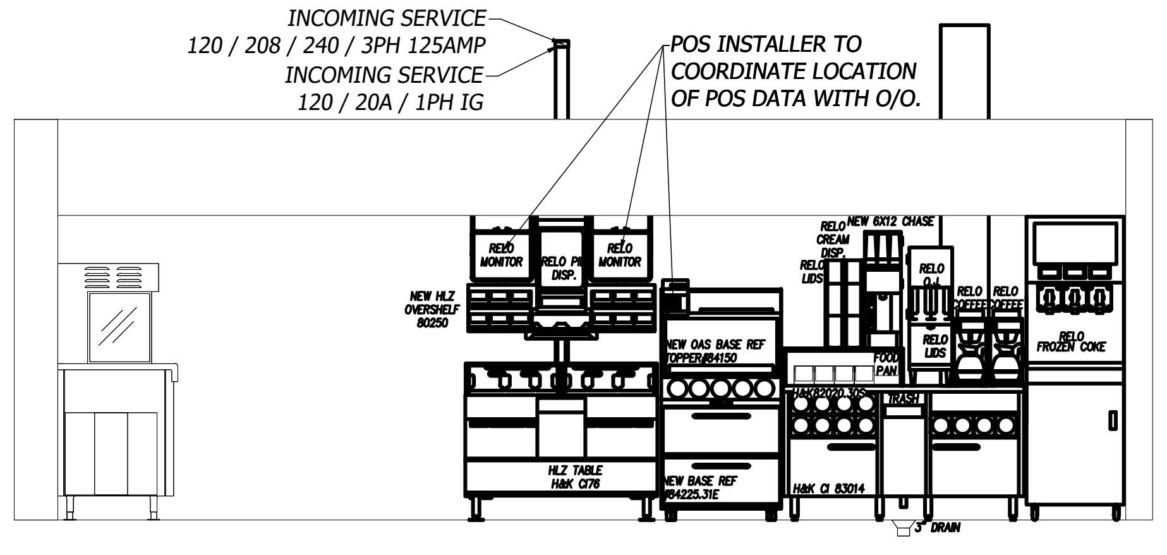
INCOMING SERVICE
120 / 208 / 240 / 3PH 125AMP
INCOMING SERVICE
120 / 20A / 1PH IG
POS INSTALLER TO COORDINATE LOCATION OF POS DATA WITH O/O.

A CENTER ISLAND ROUGH-IN

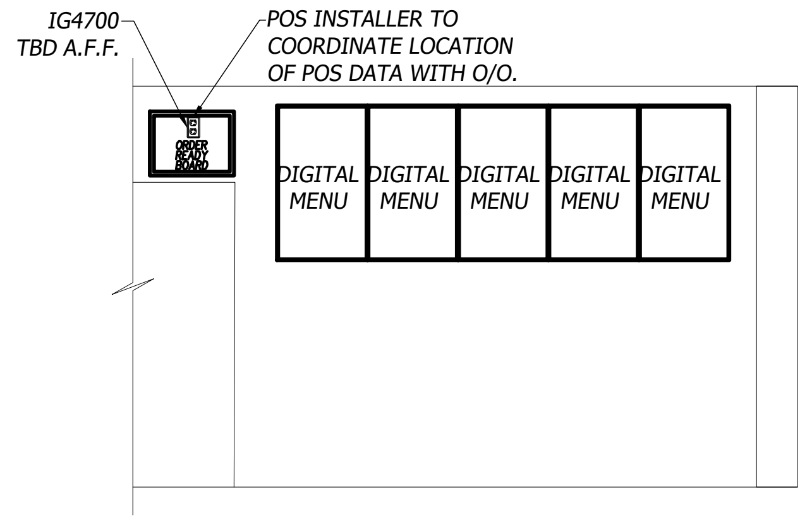

B S.A.M. WALL ROUGH-IN ELEVATION

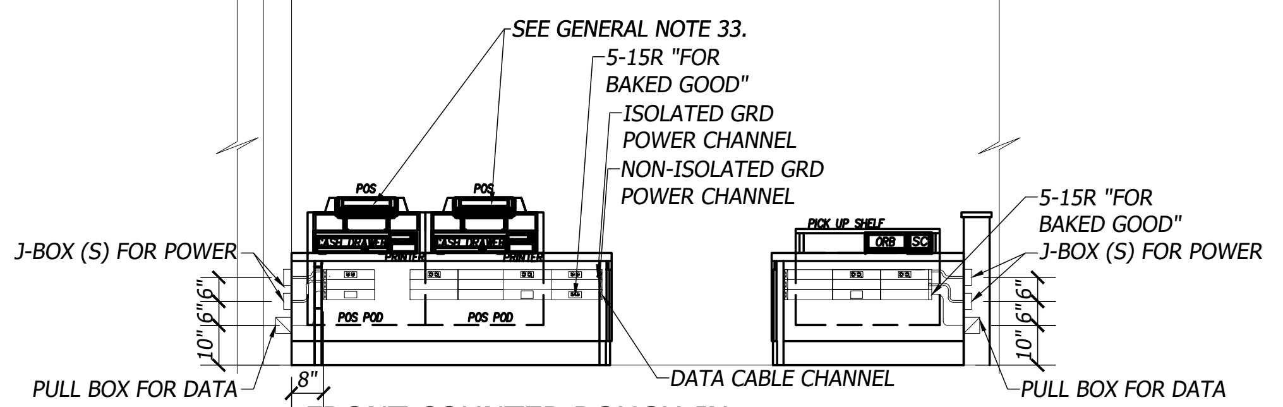

C FRONT COUNTER ROUGH-IN

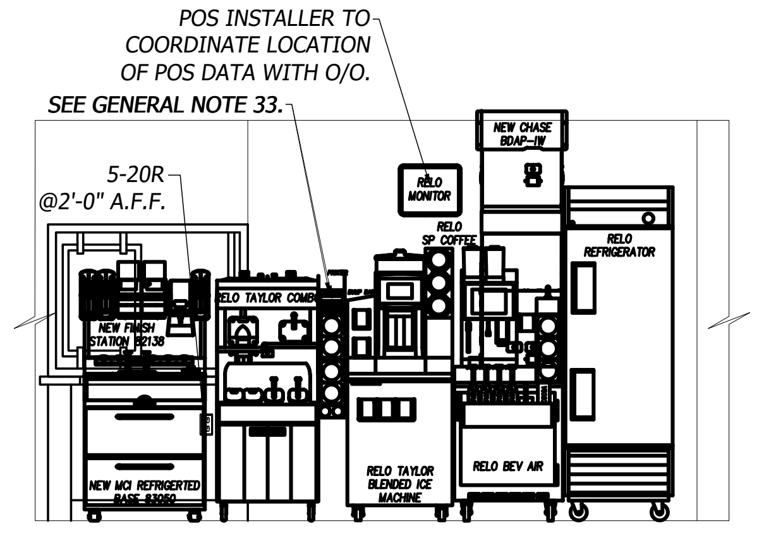

D BDAP ROUGH-IN ELEVATION

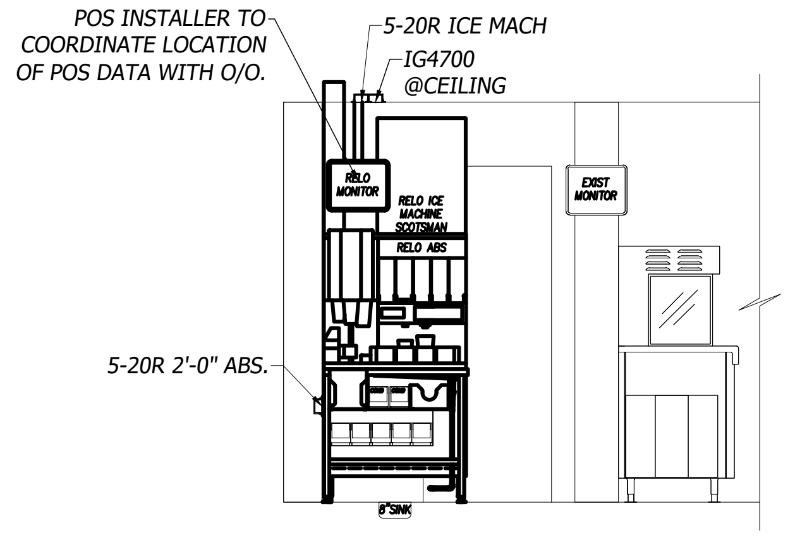

E DRIVE THRU ROUGH-IN

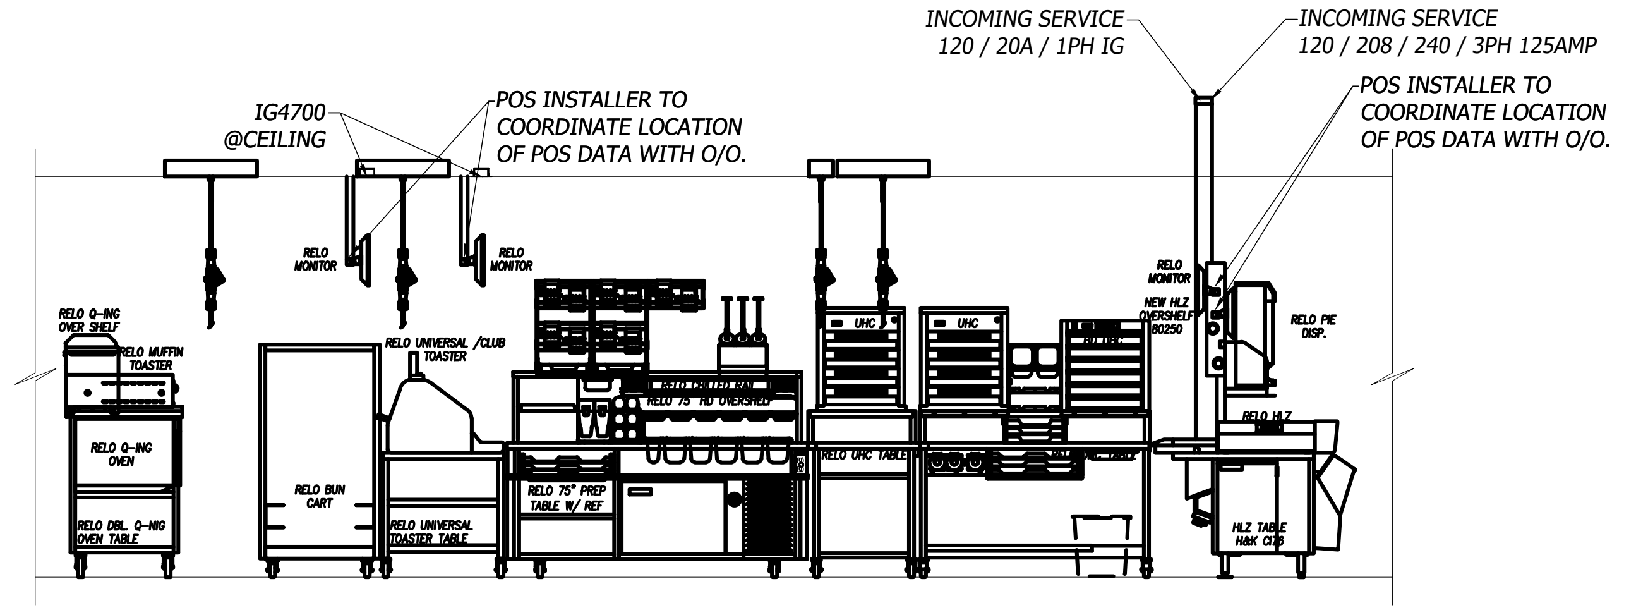
IG4700 @CEILING
POS INSTALLER TO COORDINATE LOCATION OF POS DATA WITH O/O.
INCOMING SERVICE
120 / 20A / 1PH IG
INCOMING SERVICE
120 / 208 / 240 / 3PH 125AMP
POS INSTALLER TO COORDINATE LOCATION OF POS DATA WITH O/O.

F PREP LINE ROUGH-IN

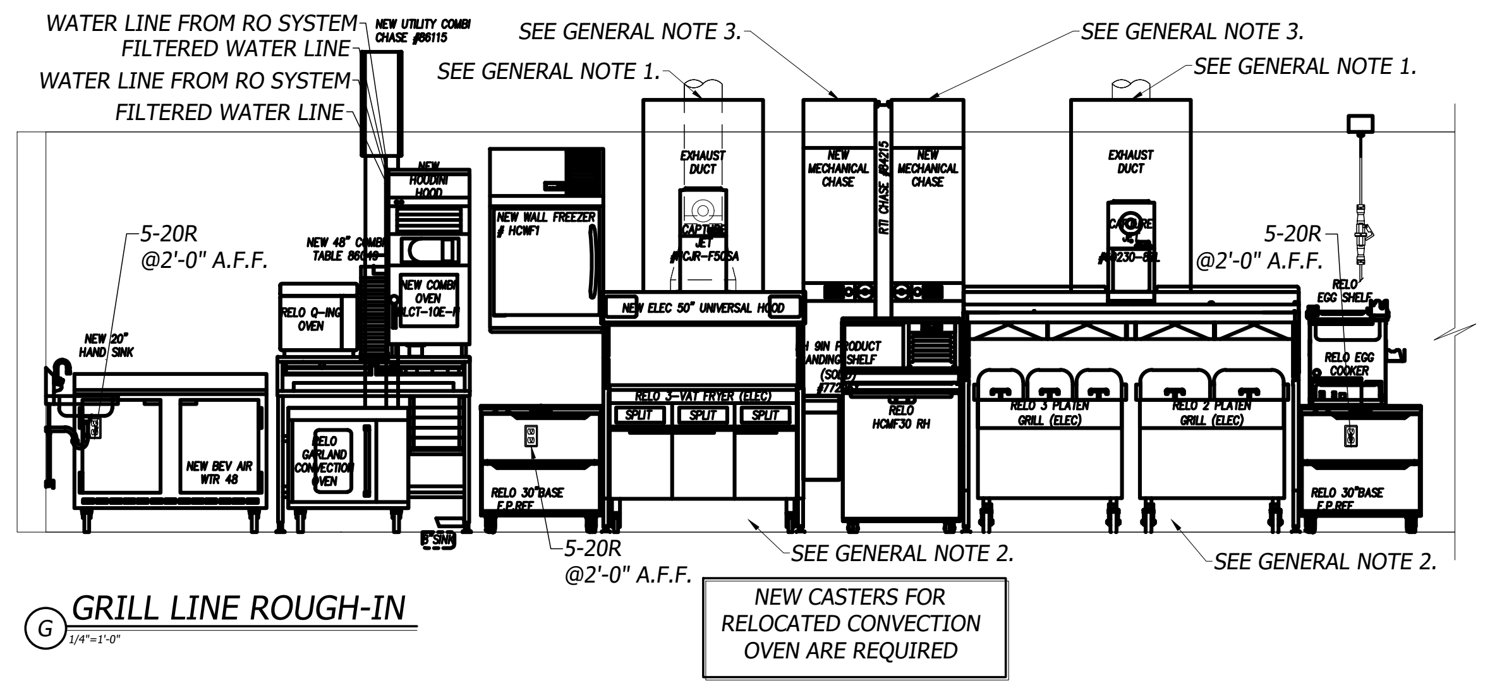

G GRILL LINE ROUGH-IN

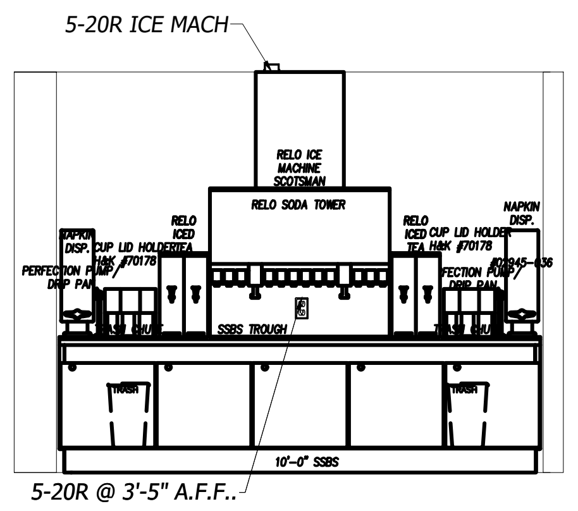

H SSBS ROUGH-IN ELEVATION

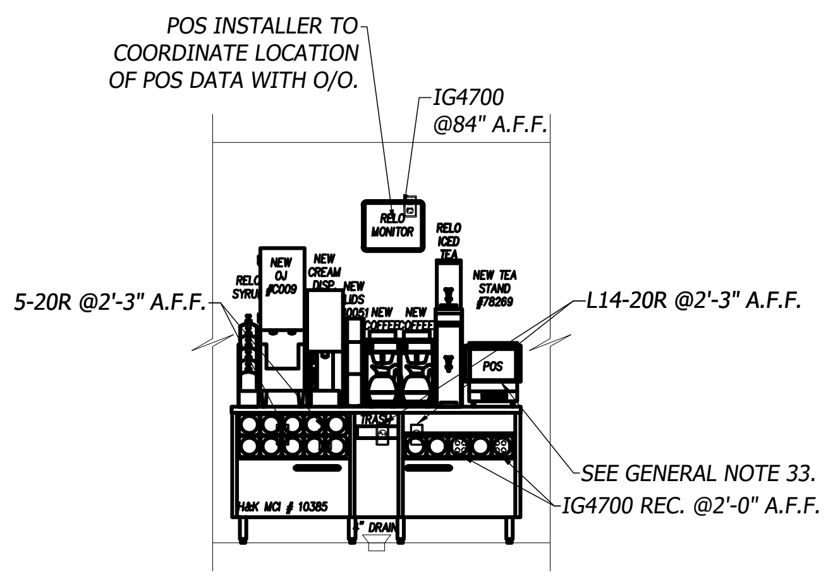
POS INSTALLER TO COORDINATE LOCATION OF POS DATA WITH O/O.
IG4700 @84" A.F.F.
5-20R @2'-3" A.F.F.
L14-20R @2'-3" A.F.F.
SEE GENERAL NOTE 33.
IG4700 REC. @2'-0" A.F.F.

I DRIVE THRU ROUGH-IN

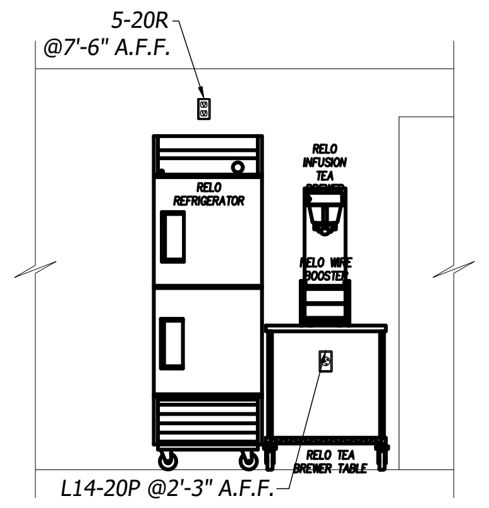

J TEA BREWER ROUGH-IN ELEVATION

GENERAL NOTES

1) USE EXISTING ROOF OPENINGS UNLESS OTHERWISE NOTED ON SCOPE OF WORK. IF NEW EXHAUST FAN ROOF OPENING IS REQUIRED, GC TO VERIFY PROPOSED ROOF OPENING LOCATION IS LOCATED A MIN. OF 10'-0" FROM HVAC AIR INTAKE. GC TO CUT NEW ROOF OPENING AND INSTALL NEW CURB AND FAN. H&K INSTALLER TO INSTALL NEW DUCT. GC TO WRAP DUCT OR CONSTRUCT ENCLOSURE IF REQUIRED BY LOCAL CODES. EC TO WIRE EXHAUST FAN TO ANSUL INTERLOCK SYSTEM.

2) KITCHEN INSTALLER TO MOUNT RACEWAY BELOW HOOD. EC TO MAKE FINAL CONNECTIONS FROM RACEWAY TO TERMINAL BLOCK INSIDE CHASE. IF GAS, KITCHEN INSTALLER TO WALL MOUNT GAS MANIFOLD BELOW HOOD. PC TO INSTALL QUICK DISCONNECT LINES AND MAKE FINAL CONNECTIONS TO IN-BOUND GAS LINE FROM CHASE AND TO INDIVIDUAL APPLIANCES.

3) ALL UTILITIES FOR APPLIANCES BELOW HOOD TO RUN OVERHEAD AND DOWN MECHANICAL CHASE. EC TO MAKE FINAL CONNECTIONS TO TERMINAL BLOCK INSIDE CHASE. IF GAS, PC TO MAKE FINAL CONNECTIONS AT GAS MANIFOLD.

4) IF CHASE IS RELOCATED, GC TO COORDINATE MODIFICATION OF ANSUL SYSTEM WITH ANSUL. RELOCATE OR PROVIDE NEW UTILITIES AS NEEDED.

5) GC TO VERIFY ALL EXISTING UTILITIES AND STRUCTURAL FLOOR LOADING CONDITIONS. REMOVE, CLOSE, SEAL, CAP AND/OR RELOCATE EXISTING LINES, DRAINS & UTILITIES. RUN DRAIN LINES TO EXISTING FLOOR DRAINS IF POSSIBLE, OR RELOCATE/INSTALL NEW FLOOR DRAINS, GAS LINES, AND SLEEVES AS NEEDED. THE GC SHALL COORDINATE ALL FINAL CONNECTIONS TO EQUIPMENT WHERE APPLICABLE.

6) GC TO REMOVE, CLOSE, SEAL, CAP, RELOCATE, OR INSTALL NEW LINES, DRAINS, RECEPTACLES, CORDS, UTILITIES, ROOF OPENINGS AS NEEDED FOR NEW AND RELOCATED EQUIPMENT. GC TO PATCH, SEAL AND/OR FINISH WALL, FLOOR, CEILING AND/OR ROOF AS NECESSARY TO MATCH EXISTING.

7) GC AND INSTALLER TO VERIFY LOCATION OF EXISTING EQUIPMENT TO REMAIN IN RELATION TO NEW AND RELOCATED EQUIPMENT.

8) REMOVE AND REPLACE DAMAGED QUARRY TILE FLOORING ADJACENT TO THE PROJECT AREA(S). MATCH EXISTING QUARRY TILE WHERE PATCHING DAMAGED TILE OR WHERE EXTENDING THE TILE FIELD IN NEW FLOOR AREAS.

9) IN THE EVENT REMOVAL OR RELOCATION OF EQUIPMENT RESULTS IN EXPOSING EXISTING KITCHEN FLOOR TILE THAT IS NOT ABRASIVE, GC SHALL REPLACE ALL EXISTING SMOOTH KITCHEN QUARRY TILE WITH ABRASIVE QUARRY TILE. SUCH REPLACEMENT TILE SHALL BE LOCATED, AT A MINIMUM, IN FRONT OF ALL GRILLS, FRYERS, BAGGING STATIONS, SINKS OR ANY LOCATION WHERE GREASE OR WATER CAN ACCUMULATE ON THE FLOOR CAUSING A SLIP AND FALL HAZARD. THE TILE SHALL EXTEND A MINIMUM OF ONE TILE COURSE UNDER THE EDGE OF THE FIXTURE OR EQUIPMENT AND EXTEND THE ENTIRE LENGTH OF THE FIXTURE OR EQUIPMENT.

10) INSTALLER TO INSTALL NEW AND RELOCATED EQUIPMENT, GC TO MAKE FINAL CONNECTIONS.

11) ALL INTERIOR FINISHES SHALL BE COORDINATED WITH DECOR & SEATING DRAWINGS BY OTHERS.

12) GC TO OBTAIN ALL PERMITS REQUIRED PER LOCAL CODE.

13) ALL WORK SHALL COMPLY WITH ALL APPLICABLE STATE AND LOCAL HEALTH, SAFETY AND CONSTRUCTION CODES. G.C., E.C., P.C. TO VERIFY THAT ALL KITCHEN EQUIPMENT, SAFETY AND INTERLOCK UTILITIES ARE FUNCTIONAL AND IN CONFORMANCE WITH ALL LOCAL CODES PRIOR TO COMPLETION OF REMODEL. G.C. TO COORDINATE ANY CORRECTIONS OF ANY DEFICIENCIES WITH McDONALD'S CONSTRUCTION, SUBCONTRACTORS, AND/OR OWNER/OPERATOR.

14) ALL ELECTRICAL MATERIAL USED ON THIS PROJECT SHALL BE "UL" LISTED AND LABELED.

15) ALL DIMENSIONS SHOWN ARE TAKEN FROM FACE OF WALL FINISH. THE GC/ALL TRADES SHALL MAKE NECESSARY DIMENSIONAL ALLOWANCES.

16) ALL J-BOXES, DCO'S, AND OTHER ELECTRICAL DEVICES SHOWN SHALL BE RECESSED MOUNTED INTO A WALL, FLOOR OR CEILING UNLESS SPECIFICALLY NOTED OTHERWISE.

17) ALL RECEPTACLES (EXCEPT SPECIFIED HUBBLE PIN AND SLEEVE) SHALL BE FURNISHED BY THE E.C. THE RECEPTACLES INCLUDING PIN AND SLEEVE TYPE SHALL BE INSTALLED BY THE EC.

18) EC SHALL PROVIDE AND INSTALL STAINLESS COVER PLATES ON ALL RECEPTACLES AND J-BOXES. ADDITIONALLY, EC SHALL PROVIDE AND INSTALL ORANGE NYLON COVER PLATES MARKED "COMPUTER ONLY" ON ALL ISOLATED GROUND/DEDICATED RECEPTACLES.

19) POWER AND CONTROL CORDS ARE FURNISHED WITH KITCHEN APPLIANCES. THE EC SHALL CONNECT CORD SETS TO APPLIANCES AS REQUIRED.

20) MOST KITCHEN REMODELS WILL REQUIRE SOME LEVEL OF CEILING REPAIR. THIS WILL BE THE RESPONIBILITY OF THE GC.

21) ALL HOLES IN FRONT COUNTER FOR POS CORDS AND CABLES SHALL BE LOCATED BY OWNER AND DRILLED BY GC.

22) EC SHALL PROVIDE A DUPLEX RECEPTACLE AND LOW VOLTAGE BROADBAND CONNECTION FOR THE INSTALLATION OF PLASMA TELEVISIONS. COORDINATE EXACT LOCATIONS WITH PM & DECOR COMPANY. FOR BROADBAND CONNECTION, EC SHALL PROVIDE A 4 X 4 BOX WITH A ¾" CONDUIT STUB-UP WITH A BUSHING INTO ACCESSIBLE CEILING SPACE.

23) WHERE PIPING IS LOCATED WITHIN WALL CAVITIES, ACCESS TO THE CLEANOUTS SHALL BE PROVIDED.

24) DIMENSIONS SHOWING THE LOCATION OF DRAINS AND FLOOR SINKS ARE CENTERLINE DIMENSIONS.

25) GAS PIPING SHALL NOT PENETRATE ANY FIRE-RATED CHASE, SHAFT, DUCTWORK OR PLENUM.

26) GC TO RE-BALANCE THE HVAC SYSTEM AFTER ANY EXHAUST HOOD HAS BEEN REPLACED OR RELOCATED.

27) ALL EQUIPMENT SHALL BE INSTALLED IN ACCORDANCE WITH ITS LISTING AND/OR THE MANUFACTURER'S INSTALLATION INSTRUCTIONS.

28) UPON COMPLETION OF INSTALLATION, THE GAS PIPING SYSTEM SHALL BE PURGED OF DELETERIOUS MATERIAL AND SHALL BE PRESSURE TESTED. IF THE MINIMUM PRESSURES ARE NOT MET, THIS SHALL BE IMMEDIATELY REPORTED TO THE MCDONALD'S CONSTRUCTION MANAGER.

29) FLEXIBLE DUCTWORK SHALL NOT PENETRATE WALLS. SHEET METAL DUCTWORK IS REQUIRED AT ALL FIRE-RATED AND DRAFT STOP WALL PENETRATIONS.

30) ALL GREASE EXHAUST DUCTWORK SEAMS AND JOINTS SHALL BE CONTINUOUSLY WELDED WATER-TIGHT ON THE EXTERNAL SURFACE OF THE DUCT SYSTEM. ALL WELDING SHALL BE PERFORMED BY A CERTIFIED WELDER.

31) IN THE EVENT OF ADDITIONAL FRYER CAPACITY, THE O/O MUST ENGAGE LICENSED MECHANICAL ENGINEER. THE M/E WILL BE REQUIRED TO ASSESS THE EXISTING EXHAUST HOOD FAN TO ENSURE IT IS CAPABLE OF HIGHER AIRFLOW AT A POTENTIALLY HIGHER STATIC PRESSURE. CONSTRUCTION DRAWINGS WILL BE REQUIRED OF THE M/E FOR PERMITTING. AFTER INSTALLATION, A CERTIFIED TEST AND BALANCE COMPANY WILL BE REQUIRED TO AIR BALANCE THE NEW AND ANY AFFECTED ROOF-TOP HVAC EQUIPMENT DEEMED AS PART OF THE SCOPE OF WORK BY THE M/E.

32) ALL ROOF-TOP CONDENSING UNITS THAT DISCHARGE HORIZONTALLY SHALL BE ORIENTED SUCH THAT THE DISCHARGE DOES NOT BLOW IN THE DIRECTION OF AN OUTDOOR AIR INTAKE.

33) POS INSTALLER TO COORDINATE RELOCATION OF POS SYSTEM WITH O/O AND MCDONALDS CONSTRUCTION. ALL CABLES FURNISHED AND INSTALLED BY POS SUPPLIER.

34) NEW POS(S) ARE SHOWN TO MEET NATIONAL BUILDING AND EQUIPMENT STANDARDS PER MCDONALD'S . FINAL LOCATION OF NEW POS(S) TO BE COORDINATED WITH O/O. POS INSTALLER TO COORDINATE LOCATION OF POS SYSTEM WITH O/O AND MCDONALDS CONSTRUCTION. ALL CABLES FURNISHED AND INSTALLED BY POS SUPPLIER.

35) PLUMBING FOR COMBI OVENS TO BE ROUTED TO FLOOR SINK DRAIN. GC TO VERIFY IF SINK HAS A GREASE INTERCEPT.

SYMBOL LEGEND

⏀	DUPLEX OUTLET (SB OR TL)	─	OPTIONAL EQUIPMENT
⏀	SINGLE OUTLET (SB OR TL)	━	NEW EQUIPMENT ON EQUIPMENT PLAN
⊕	QUAD OUTLET (SB OR TL)	━	RELOCATED EQUIPMENT ON EQUIPMENT PLAN
△	SPECIAL OUTLET (SEE SCHEDULE)	– – –	EXISTING EQUIPMENT
Ⓙ	J-BOX	─	EQUIPMENT ON ROUGH-IN PLAN
▣	DATA CABLE	— — —	EXISTING TRUSSES
◯	EXHAUST DUCT ABOVE HOOD	─	SERVICE AREA
◯	EXHAUST DUCT ABOVE HOOD	━ ━ ━	NEW MENU BOARD VALANCE
◎	SLEEVE	■	EXISTING FULL WALL
⊛	REFRIGERATION LINES	─	EXISTING LOW WALL
○	WATER OR GAS LINE	▩	NEW FULL WALL
○	CLEAN OUT	▨	NEW LOW WALL
▤	FLOOR SINK		
⊠	FLOOR DRAIN		

REV	DATE	DESCRIPTION	BY

ENGINEER OF RECORD:

4/12/19

PREPARED BY:
CORE STATES
GROUP
CORESTATES, INC.
1700 Industrial Drive
Suite B
Rogers, AR 72756
479.986.4400
www.core-eng.com

PREPARED FOR:
McDonald's USA, LLC

These drawings and specifications are the confidential and proprietary property of McDonald's USA, LLC and shall not be copied or reproduced without written authorization. The contract documents were prepared for use on this specific site in conjunction with its issue date and are not suitable for use on a different site or at a later time. Use of these drawings for reference or example on another project requires the services of properly licensed architects and engineers. Reproduction of the contract documents for reuse on another project is not authorized.

DRAWN BY
CHR

STD ISSUE DATE
MAY 2018

REVIEWED BY
J.FERGUSON

DATE ISSUED
10/12/18

C.S.G. PROJECT #
MCD–24772

TITLE
MRP PROGRAM
CORE 16 2.0

DESCRIPTION
EXISTING MASONRY WALL CONSTRUCTION
EXISTING WOOD ROOF TRUSSES
TILE ARCADES – FRONT, ENTRY

SITE ID
024–0294

SITE ADDRESS
815 EASTLAND DRIVE
JEFFERSON CITY, MO 65101

SHEET NO.
K2.0
ELEC ROUGH IN

EQUIPMENT SCHEDULE

Count	ITEM #	OPT	ITEM DESCRIPTION	MFGR	UNIT ID	UL LIST	NSF LIST	FURN BY	REMARKS
1	1.13	N	MODULAR FRONT COUNTER OVERSHELF	DÉCOR	MCF-OS	-	2	GC	-
2	1.18	N	MODULAR FRONT COUNTER BASE	DÉCOR	MFC	-	2	GC	SIZE VARY PER MATRIX
1	1.31	N	MODULAR FRONT COUNTER ACCESSORY RISER	DÉCOR	MFC-AR				
1	7.02	N	10'-0" SELF-SERVE BEVERAGE STATION	H&K	H&K #	-	2	KES	-
1	9.00	N	UTILITY CHASE	H&K	H&K #	-	2	KES	-
1	9.14	N	UTILITY CHASE - D/T BEVERAGE CABINET VERSION 20"x5"x66"	Wasserstrom	SEE ELEV	-	2	KES	4 SECTION CHASE FOR BUYOUT RECEPT., POS, CO2, WATER
1	9.93	N	NEW UTILITY CHASE - COMBI WATER- POWER	H&K	SEE ELEV	-	-	KES	-
1	9.98	N	UTILITY CHASE - WALL MOUNTED F/ WATER LINE	H&K	SEE ELEV	-	2	KES	CHASE FOR BULK OIL LINES, MOUNT AT 2'-0"
1	10.04	N	CO2 DRIVEN KETCHUP DISPENSER	PERFECTION	-	-	2	KES	-
2	10.93	N	CUP LID HOLDER	H&K	SEE ELEV	-	2	KES	-
2	21.01	N	COFFEE BREWER	BUNN	AXIOMP-DV-3	-	-	KES	-
1	21.92	N	COMBO CUPS BRACKET FOR BUMP BAR & PRINTER	H&K	SEE ELEV	-	3	KES	-
1	23.05	N	COFFEE CREAM DISPENSER	SILVER KING	SEE ELEV	SA32728	20	KES	-
1	24.01	N	ORANGE JUICE DISPENSER, DUAL FLAVOR	TAYLOR	C009	SA4632	18	KES	-
2	44.03	N	5' CENTER ISLAND, BEV HEIGHT	H&K	SEE ELEV	-	2	KES	-
1	44.13	N	CENTER ISLAND- 48" HLZ HEIGHT	H&K	SEE ELEV	-	2	KES	-
1	44.29	N	BREAKER PANEL- 125 AMP - 3 PHASE EQUIPMENT MOUNTED	H&K	H&K #	E99018	-	KES	-
1	44.30	N	BREAKER PANEL- 125 AMP - 1 PHASE EQUIPMENT MOUNTED	H&K	H&K #	E99018	-	KES	-
1	45.47	N	MOBILE CUP CART	H&K	SEE ELEV	-	-	-	-
1	51.06	N	CUP LID HOLDER-SINGLE WIDE, 3 TIER	H&K	SEE ELEV	-	2	KES	-
1	73.00	N	UNIVERSAL EXHAUST HOOD (R.H.) ELECTRIC 3-VAT FRYER	H&K	H&K # UH50	MH12755	2	KES	-
2	80.00	N	MECHANICAL CHASE, 9"x18" SGCL.	H&K	H&K #MC	E163328	2	KES	-
1	81.02	N	PRODUCT LANDING SHELF - CUT OUT TOP	H&K	H&K #	-	2	KES	-
1	90.80	N	CAPTURE JET FOR 3 VAT FRYER	HALTON	SEE ELEV	-	-	-	-
1	90.83	N	CAPTURE JET FOR 83" HOOD (2)GRILLS	HALTON	SEE ELEV	-	-	-	-
1	91.00	N	WALL MOUNT FREEZER-SINGLE WIDE	H&K	H&K # HCWF1	SA7329	7	KES	AIR-COOLED, SELF-CONTAINED - MOUNT BOTTOM AT 54" AFF
1	94.15	N	UNIVERSAL EXHAUST HOOD (L.H.) 2-ELEC FULL-CLAM GRILLS (WITH CAPTURE JET)	H&K	H&K # UH83	MH12755	2	KES	-
1	119.11	N	COMBI CELL TABLE	H&K	SEE ELEV	-	3	KES	-
1	130.00	N	COMBI-BLODGETT OVEN	BLODGETT	SEE ELEV	-	-	KES	-
1	141.10	N	HOUDINI - OVEN VENTLESS HOOD	HOUDINI	SEE ELEV	-	-	KES	-
1	171.07	N	WALK-IN COOLER / FREEZER WITH FLOORS	NORLAKE	-	E42763	7	KES	-
1	174.00	N	REMOTE CONDENSING UNIT	BOHN	MAC-8GB	SA4272	-	KES	BEACON SYSTEM
1	175.08	N	COOLER EVAPORATOR - AIR-COOLED	BOHN	ADT104BEB2N6MK	SA1525	-	KES	BEACON SYSTEM EVAPORATOR
1	176.21	N	FREEZER EVAPORATOR - AIR-COOLED	BOHN	LET180BEB2N6MK	SA1525	-	KES	BEACON SYSTEM EVAPORATOR
1	181.04	N	REFRIGERATOR - WORKTOP - 48" WIDE	BEV AIR/DELFIELD	WTR48-23/ST4048	SA2651	7	KES	-
3	194.36	N	DRY SHELVING 26"x100"x84" H.-4-TIER - MOBILE	DENSTOR	-	-	2	MANUFACTURER	-
2	195.36	N	DRY SHELVING 26"x100"x84" H.-5-TIER- MOBILE	DENSTOR	-	-	2	MANUFACTURER	-
1	195.51	N	DRY SHELVING 26"x100"x84" H.- 5-TIER- FIXED	DENSTOR	-	-	2	MANUFACTURER	-
2	207.09	N	30" BASE REFRIGERATOR	H&K	SEE ELEV	SA4044	7	KES	-
1	207.10	N	FINISHING STATION	FRANKE	SEE ELEV	-	7	KES	IF USED IN CONJUNCTION WITH THE BASE REFRIGERATOR, BOTH ITEMS CAN SHARE A DUPLEX RECEPTACLE
2	216.03	N	STANDOFF FOR COFFEE AND BLENDED ICE MACHINE	H&K	H&K # 84201	-	-	-	INSTALL SHELF 2'-6" AFF
1	216.04	N	ORB MONITOR (MINI)	-	-	-	-	OWNER	-
1	216.07	N	ORB SCANNER	OWNER	-	-	-	OWNER	UNDER COUNTER BRACKET BY POS SUPPLIER
1	217.00	N	PARK/SERVE/ROTATE BUMP BAR	BY OWNER	BY OWNER	-	-	OWNER	GC/POS INSTALLER TO COORDINATE RELOCATION W/ O/O
1	219.00	N	POS - RECEIPT PRINTER	POS	POS	OEM	-	OWNER	SHELF REQUIRED FOR FRONT COUNTER APPLICATIONS
1	700.01	N	HAND SINK 18 x 20"	GC	18" x 20"	-	-	GC	-
1	7000.15	N	DUAL POINT OVERSHELF (HLZ)	H&K	80250	-	-	KES	OPTIONAL EQUIPMENT - VERIFY ORDER
1	7000.32	N	RISER SHELF 18" - 30" (CENTER ISLAND)	H&K	-	-	2	KES	-
1	7003.00	N	BASE REF. SHELF & DUAL POINT OAS @ C.I (WITH CUPS)	H&K	H&K #84150	-	-	KES	-
5	8004.12	R	RELOCATED DIGITAL MENUBOARD	-	-	-	-	OWNER	EQP. INSTLR. TO RELOCATE EQUIPMENT, GC TO RELO UTILITIES AS NEEDED
1	8010.04	R	RELOCATED CO2 DRIVEN KETCHUP DISPENSER	-	-	-	-	OWNER	EQP. INSTLR. TO RELOCATE EQUIPMENT, GC TO RELO UTILITIES AS NEEDED
1	8010.93	R	RELOCATED CUP LID HOLDER	-	-	-	-	OWNER	EQP. INSTLR. TO RELOCATE EQUIPMENT
1	8010.96	R	RELOCATED NAPKIN DISPENSER	-	-	-	-	OWNER	EQP. INSTLR. TO RELOCATE EQUIPMENT
1	8020.00	R	RELOCATED AUTOMATED BEVERAGE SYSTEM	-	-	-	-	OWNER	EQP. INSTLR. TO RELOCATE EQUIPMENT, GC TO RELO UTILITIES AS NEEDED
2	8021.01	R	RELOCATED COFFEE BREWER	-	-	-	-	OWNER	EQP. INSTLR. TO RELOCATE EQUIPMENT, GC TO RELO UTILITIES AS NEEDED
1	8021.10	R	RELOCATED SPECIALTY COFFEE	-	-	-	-	OWNER	EQP. INSTLR. TO RELOCATE EQUIPMENT, GC TO RELO UTILITIES AS NEEDED
1	8021.11	R	RELOCATED BLENDED ICE MACHINE	-	-	-	-	OWNER	EQP. INSTLR. TO RELOCATE EQUIPMENT, GC TO RELO UTILITIES AS NEEDED
1	8023.05	R	RELOCATED COFFEE CREAM DISPENSER	-	-	-	-	OWNER	EQP. INSTLR. TO RELOCATE EQUIPMENT, GC TO RELO UTILITIES AS NEEDED
1	8024.01	R	RELOCATED ORANGE JUICE DISPENSER, DUAL FLAVOR	-	-	-	-	OWNER	EQP. INSTLR. TO RELOCATE EQUIPMENT, GC TO RELO UTILITIES AS NEEDED
6	8025.01	R	RELOCATED ICED BEVERAGE DISPENSER	-	-	-	-	OWNER	EQP. INSTLR. TO RELOCATE EQUIPMENT
1	8025.02	R	RELOCATED ICED TEA BREWER	-	-	-	-	OWNER	EQP. INSTLR. TO RELOCATE EQUIPMENT, GC TO RELO UTILITIES AS NEEDED
1	8025.95	R	RELOCATED ICED TEA DISPENSER - 2 TIER STAND	-	-	-	-	OWNER	EQP. INSTLR. TO RELOCATE EQUIPMENT
1	8028.13	R	RELOCATED SODA TOWER	-	-	-	-	OWNER	EQP. INSTLR. TO RELOCATE EQUIPMENT, GC TO RELO UTILITIES AS NEEDED
2	8039.22	R	RELOCATED ICE MACHINE	-	-	-	-	OWNER	EQP. INSTLR. TO RELOCATE EQUIPMENT, GC TO RELO UTILITIES AS NEEDED
2	8043.15	R	RELOCATED HEATED LANDING ZONE	-	-	-	-	OWNER	EQP. INSTLR. TO RELOCATE EQUIPMENT, GC TO RELO UTILITIES AS NEEDED
1	8046.00	R	RELOCATED CUP DISPENSER VERTICAL F/ 3 TUBES	-	-	-	-	OWNER	EQP. INSTLR. TO RELOCATE EQUIPMENT
1	8046.02	R	RELOCATED SYRUP BOTTLE RACK - 5-SYRUP PUMPS, HORIZONTAL	-	-	-	-	OWNER	EQP. INSTLR. TO RELOCATE EQUIPMENT
2	8051.03	R	RELOCATED CUP LID HOLDER-SINGLE WIDE, 8" HIGH	-	-	-	-	OWNER	EQP. INSTLR. TO RELOCATE EQUIPMENT
1	8065.29	R	RELOCATED 3-VAT FRYER - ELECTRIC - S/S/S	-	-	-	-	OWNER	EQP. INSTLR. TO RELOCATE EQUIPMENT, GC TO RELO UTILITIES AS NEEDED
1	8096.11	R	RELOCATED 36" CLAMSHELL GRILL - 3 PLATEN - ELECTRIC	-	-	-	-	OWNER	EQP. INSTLR. TO RELOCATE EQUIPMENT, GC TO RELO UTILITIES AS NEEDED
1	8096.15	R	RELOCATED 36" CLAMSHELL GRILL - 2 PLATEN - ELECTRIC	-	-	-	-	OWNER	EQP. INSTLR. TO RELOCATE EQUIPMENT, GC TO RELO UTILITIES AS NEEDED
1	8097.07	R	RELOCATED GRILL SIDE MEAT FREEZER - DOUBLE WIDE	-	-	-	-	OWNER	AIR-COOLED, SELF-CONTAINED
1	8098.14	R	RELOCATED EGG COOKER SHELF	-	-	-	-	OWNER	EQP. INSTLR. TO RELOCATE EQUIPMENT
1	8099.96	R	RELOCATED TEA BREWER TABLE 30 X 36	-	-	-	-	OWNER	EQP. INSTLR. TO RELOCATE EQUIPMENT
1	8111.10	R	RELOCATED BUN BOX	-	-	-	-	OWNER	EQP. INSTLR. TO RELOCATE EQUIPMENT
2	8116.01	R	RELOCATED UNIVERSAL HOLDING CABINET - 2-SIDED - PIN & SLEEVE	-	-	-	-	OWNER	EQP. INSTLR. TO RELOCATE EQUIPMENT, GC TO RELO UTILITIES AS NEEDED
1	8116.23	R	RELOCATED UNIVERSAL HOLDING CABINET - HD - 2-SIDED - P&S	-	-	-	-	OWNER	EQP. INSTLR. TO RELOCATE EQUIPMENT, GC TO RELO UTILITIES AS NEEDED
2	8117.13	R	RELOCATED UHC TABLE - 2 SIDED	-	-	-	-	OWNER	EQP. INSTLR. TO RELOCATE EQUIPMENT, GC TO RELO UTILITIES AS NEEDED
3	8118.00	R	RELOCATED Q'ING OVEN	-	-	-	-	OWNER	EQP. INSTLR. TO RELOCATE EQUIPMENT, GC TO RELO UTILITIES AS NEEDED
1	8119.08	R	RELOCATED Q'ING OVEN BREAKFAST TABLE	-	-	-	-	OWNER	EQP. INSTLR. TO RELOCATE EQUIPMENT
1	8119.09	R	RELOCATED Q'ING OVEN BREAKFAST TABLE RETROFIT SHELF	-	-	-	-	OWNER	EQP. INSTLR. TO RELOCATE EQUIPMENT
1	8120.06	R	RELOCATED TOASTER TABLE	-	-	-	-	OWNER	EQP. INSTLR. TO RELOCATE EQUIPMENT
1	8121.00	R	RELOCATED MUFFIN TOASTER - PIN & SLEEVE	-	-	-	-	OWNER	EQP. INSTLR. TO RELOCATE EQUIPMENT, GC TO RELO UTILITIES AS NEEDED
1	8122.22	R	RELOCATED UNIVERSAL TOASTER - P&S	-	-	-	-	OWNER	EQP. INSTLR. TO RELOCATE EQUIPMENT, GC TO RELO UTILITIES AS NEEDED
1	8122.23	R	RELOCATED CLUB TOASTER - P&S	-	-	-	-	OWNER	EQP. INSTLR. TO RELOCATE EQUIPMENT, GC TO RELO UTILITIES AS NEEDED
1	8123.24	R	RELOCATED PREP TABLE (2 SIDED) HD 34" x 75"	-	-	-	-	OWNER	EQP. INSTLR. TO RELOCATE EQUIPMENT, GC TO RELO UTILITIES AS NEEDED
1	8131.02	R	RELOCATED BISCUIT OVEN	-	-	-	-	OWNER	EQP. INSTLR. TO RELOCATE EQUIPMENT, GC TO RELO UTILITIES AS NEEDED
1	8143.00	R	RELOCATED EGG COOKER	-	-	-	-	OWNER	EQP. INSTLR. TO RELOCATE EQUIPMENT, GC TO RELO UTILITIES AS NEEDED
2	8177.00	R	RELOCATED REACH-IN REFRIGERATOR-SINGLE WIDE	-	-	-	-	OWNER	EQP. INSTLR. TO RELOCATE EQUIPMENT, GC TO RELO UTILITIES AS NEEDED
1	8179.01	R	RELOCATED REFRIGERATOR - PASS-THRU	-	-	-	-	OWNER	EQP. INSTLR. TO RELOCATE EQUIPMENT, GC TO RELO UTILITIES AS NEEDED
1	8181.01	R	RELOCATED SPECIALTY COFFEE REFRIGERATOR-27" WIDE	-	-	-	-	OWNER	EQP. INSTLR. TO RELOCATE EQUIPMENT, GC TO RELO UTILITIES AS NEEDED
1	8201.98	R	RELOCATED WORK TABLE F/ ABS & CONDIMENTS	-	-	-	-	OWNER	EQP. INSTLR. TO RELOCATE EQUIPMENT, GC TO RELO UTILITIES AS NEEDED
1	8203.02	R	RELOCATED HEAT TREAT COMBINATION SHAKE/SUNDAE MACHINE	-	-	-	-	OWNER	EQP. INSTLR. TO RELOCATE EQUIPMENT, GC TO RELO UTILITIES AS NEEDED
1	8205.10	R	RELOCATED FROZEN CARBONATED BEVERAGE (FCB)	-	-	-	-	OWNER	EQP. INSTLR. TO RELOCATE EQUIPMENT, GC TO RELO UTILITIES AS NEEDED
2	8207.09	R	RELOCATED BASE REFRIGERATOR	-	-	-	-	OWNER	EQP. INSTLR. TO RELOCATE EQUIPMENT, GC TO RELO UTILITIES AS NEEDED
1	8207.90	R	RELOCATED CUP TUBES FOR HEAT TREAT MACHINE	-	-	-	-	OWNER	EQP. INSTLR. TO RELOCATE EQUIPMENT
2	8215.00	R	RELOCATED POS PC HARDWARE - FRONT COUNTER	BY OWNER	POS	OEM	-	OWNER	GC/POS INSTALLER TO COORDINATE RELOCATION W/ O/O
2	8215.98	R	RELOCATED POS PC HARDWARE - D/T	POS INSTALLER	-	OEM	-	OWNER	GC/POS INSTALLER TO COORDINATE RELOCATION W/ O/O
9	8216.00	R	RELOCATED POS - VIDEO MONITOR	POS	POS	E106786	-	OWNER	GC/POS INSTALLER TO COORDINATE LOCATION W/ O/O
1	8216.05	R	RELOCATED ORB MONITOR	BY OWNER	BY OWNER	-	-	OWNER	GC/POS INSTALLER TO COORDINATE RELOCATION W/ O/O
3	8218.00	R	RELOCATED POS - CASH DRAWER	BY OWNER	BY OWNER	OEM	-	OWNER	GC/POS INSTALLER TO COORDINATE RELOCATION W/ O/O
3	8219.00	R	RELOCATED POS - RECEIPT PRINTER	POS	POS	OEM	-	OWNER	GC/POS INSTALLER TO COORDINATE RELOCATION W/ O/O
1	8237.00	R	RELOCATED PIE DISPLAY	-	-	-	-	OWNER	EQP. INSTLR. TO RELOCATE EQUIPMENT, GC TO RELO UTILITIES AS NEEDED
5	8700.09	R	RELOCATED OEP BOX W/MOUNTING HARDWARE	-	-	-	-	OWNER	EQP. INSTLR. TO RELOCATE EQUIPMENT, GC TO RELO UTILITIES AS NEEDED
2	8700.10	R	RELOCATED BULK OIL SYSTEM	-	-	-	-	OWNER	GC TO RELOCATE AS REQUIRED
1	9002.07	E	EXISTING TRAY CART	-	-	-	-	OWNER	-
4	9009.00	E	EXISTING UTILITY CHASE	-	-	-	-	OWNER	-
1	9032.00	E	EXISTING REVERSE OSMOSIS WATER FILTRATION SYSTEM	-	-	-	-	OWNER	-
1	9032.01	E	EXISTING REVERSE OSMOSIS WATER FILTRATION SYSTEM - TANK	-	-	-	-	OWNER	-
1	9032.03	E	EXISTING WATER FILTRATION SYSTEM	-	-	-	-	OWNER	-
2	9036.00	E	EXISTING BULK COKE	-	-	-	-	OWNER	-
1	9037.00	E	EXISTING BULK CO2	-	-	-	-	OWNER	-
1	9039.09	E	EXISTING ICE MACHINE	-	-	-	-	OWNER	-
1	9065.24	E	EXISTING 3-VAT FRYER - ELECTRIC - F/F/F	-	-	-	-	OWNER	-
1	9070.91	E	EXISTING EXHAUST HOOD	-	-	-	-	OWNER	-
1	9085.05	E	EXISTING FROZEN FRY DISPENSER	-	-	-	-	OWNER	-
1	9098.01	E	EXISTING 3-TIER APPLIANCE STAND	-	-	-	-	OWNER	-
2	9111.07	E	EXISTING BUN CART	-	-	-	-	OWNER	-
1	9151.00	E	EXISTING WORK SINK - 3 COMPARTMENT	-	-	-	-	OWNER	-
1	9152.06	E	EXISTING WAREWASHER PASS THRU/CORNER UNIT	-	-	-	-	OWNER	-
1	9159.04	E	EXISTING SS TABLE	-	-	-	-	OWNER	-
1	9193.32	E	EXISTING DRY SHELVING - MOBILE	-	-	-	-	OWNER	-
1	9201.02	E	EXISTING DRIVE-THRU POS STAND W/OVERHEAD SHELVES - 21" DP x 36" L	-	-	-	-	OWNER	-
1	9201.08	E	EXISTING GREASE TRAP	-	-	-	-	OWNER	-
1	9201.10	E	EXISTING HAPPY MEAL CART - 14" x 30"	-	-	-	-	OWNER	-
2	9215.98	E	EXISTING POS PC HARDWARE - D/T	-	-	-	-	OWNER	-
1	9216.00	E	EXISTING POS - VIDEO MONITOR	-	-	-	-	OWNER	-
1	9218.00	E	EXISTING POS - CASH DRAWER	-	-	-	-	OWNER	-
1	9219.02	E	EXISTING POS - RECEIPT PRINTER	-	-	-	-	OWNER	-
1	9223.00	E	EXISTING WASHER	-	-	-	-	OWNER	-
1	9233.00	E	EXISTING WARMER	-	-	-	-	OWNER	-
1	9700.02	E	EXISTING MOP SINK	-	-	-	-	OWNER	-
1	9700.07	E	WATER HEATER - GAS	-	-	-	-	OWNER	-
1	9700.20	E	EXISTING STORAGE TANK	-	-	-	-	OWNER	-

PLUMBING SCHEDULE

Count	ITEM #	ITEM DESCRIPTION	GAS TYPE	GAS BTU	GAS SIZE	HOT WATER	COLD WATER	MISC PLBG	HGT AFF	DRAIN	REQUIREMENTS
1	130.00 P1	COMBI-BLODGETT OVEN	-	-	-	-	1/2" ID TUBING	R.O.	SEE RMKS	-	DN CHASE FROM REVERSE OSMOSIS SYSTEM. BEV INSTALLER TO CONN CW LINE, PER LOCAL CODES IF TWO OVENS ARE REQUIRED, ONE MAIN LINE CAN BE SPLIT IF NEEDED. BEV INSTALLER TO INSTALL SHUTOFF VALVE
1	130.00 P2	COMBI-BLODGETT OVEN	-	-	-	-	1/2" ID TUBING	FILTERED WATER	SEE RMKS	-	DN CHASE FROM FILTERED WATER BEV INSTALLER TO CONN CW LINE, PER LOCAL CODES IF TWO OVENS ARE REQUIRED, ONE MAIN LINE CAN BE SPLIT IF NEEDED. BEV INSTALLER TO INSTALL SHUTOFF VALVE
1	130.00 P3	COMBI-BLODGETT OVEN	-	-	-	-	-	-	SEE RMKS	1 1/2"	RUN DRAIN LINE TO FLOOR SINK PER LOCAL CODE. IF TWO OVENS REQUIRED GC TO TIE EACH DRAIN INTO ONE IF NEEDED
1	175.08 P1	COOLER EVAPORATOR - AIR-COOLED	-	-	-	-	-	3/4" LINE	-	-	3/4" CONDENSATE DRAIN LINE W/RETURN BEND & TRAP-SUPP. BY REFRIG. CONTRACTOR
1	175.08 P2	COOLER EVAPORATOR - AIR-COOLED	-	-	-	-	-	-	-	-	OPENING FOR 3/4" CONDENSATION DRAIN LINE-SEALED WEATHER TIGHT BY GC
1	175.08 P3	COOLER EVAPORATOR - AIR-COOLED	-	-	-	-	-	REFRIG LINES	-	-	RUN TO REMOTE CONDENSING UNIT-INSULATE FULL RUN LENGTH-INSTALLED BY REFRIG. CONTRACTOR
1	176.21 P1	FREEZER EVAPORATOR - AIR-COOLED	-	-	-	-	-	3/4" LINE	-	-	3/4" CONDENSATE DRAIN LINE W/RETURN BEND & TRAP-SUPP. BY REFRIG. CONTRACTOR
1	176.21 P2	FREEZER EVAPORATOR - AIR-COOLED	-	-	-	-	-	-	-	-	OPENING FOR 3/4" CONDENSATION DRAIN LINE-SEALED WEATHER TIGHT BY GC
1	176.21 P3	FREEZER EVAPORATOR - AIR-COOLED	-	-	-	-	-	REFRIG LINES	-	-	RUN TO REMOTE CONDENSING UNIT-INSULATE FULL RUN LENGTH-INSTALLED BY REFRIG. CONTRACTOR
2	21.01 P3	COFFEE BREWER	-	-	-	-	-	1/4" FILTERED	SEE RMKS	-	DN WALL FROM REVERSE OSMOSIS SYSTEM. BEV INSTALLER TO CONN CW LINE, PER LOCAL CODES
1	24.01 P2	JUICE DISPENSER, DUAL FLAVOR	-	-	-	-	1/2" FLTR	-	SEE RMKS	-	DN WALL FROM SODA TOWER CW LINE W/ RECIRC/CHIILED INSULATED BUNDLE-BSI CONN CWLINE,LOCAL CODES PERMITTING
1	700.01 P1	HAND SINK 18" X 20"	-	-	-	1/2"	1/2"	-	SEE RMKS	2 1/2" D	2" WASTE @ 1'-3" AFF WITH 1 1/2" VENT UP - WATER LINES @ 1'-10" - HW =110 DEGREES
3	701.22 P1	4" FLOOR DRAIN	-	-	-	-	-	2" VENT	-	4" DRAIN	PC TO INSTALL NEW DRAIN OR RELOCATE EXISTING AS NEEDED.
3	701.25 P1	8" X 8" FLOOR SINK WITH 1 1/2" DRAIN	-	-	-	-	-	2" VENT	-	1 1/2" DRAIN	PC TO INSTALL NEW DRAIN OR RELOCATE EXISTING AS NEEDED.
1	701.33 P1	TRENCH DRAIN (BDAP)	-	-	-	-	-	-	-	-	PC TO INSTALL NEW DRAIN OR RELOCATE EXISTIN AS NEEDED. (REINFORCED STAINLESS STEEL SLOTTED GRATE.NO-HUB BOTTOM OUTLET. BOTTOM DOME STRAINER. VANDAL-PROOF LOCKDOWN. CLOSED END CAP)
1	8020.00 P2	RELOCATED AUTOMATED BEVERAGE SYSTEM	-	-	-	-	-	6" PVC CONDUIT	SEE RMKS	-	GC TO INSTALL, ABOVE CEILING FROM SODA SYSTEM - TERMINATE AT CHASE
1	8020.00 P3	RELOCATED AUTOMATED BEVERAGE SYSTEM	-	-	-	-	-	6" DRINK COND.	SEE RMKS	-	BSI INSTALL DN CHASE FROM SODA SYSTEM, MAKE FINAL CONNECTIONS, PER LOCAL CODES
2	8021.01 P2	RELOCATED COFFEE BREWER	-	-	-	-	-	1/4" FILTERED	SEE RMKS	-	DN CHASE FROM REVERSE OSMOSIS SYSTEM. BEV INSTALLER TO CONN CW LINE, PER LOCAL CODES
1	8021.10 P2	RELOCATED SPECIALTY COFFEE	-	-	-	-	-	1/2" FILTERED	SEE RMKS	-	DN CHASE FROM REVERSE OSMOSIS SYSTEM. BEV INSTALLER TO CONN CW LINE, PER LOCAL CODES
1	8021.11 P2	RELOCATED SMOOTHIE MACHINE	-	-	-	-	-	1/2" FILTERED	SEE RMKS	-	DN CHASE FROM SODA SYSTEM. BEV INSTALLER TO CONN CW LINE, PER LOCAL CODES
1	8024.01 P1	RELOCATED JUICE DISPENSER, DUAL FLAVOR	-	-	-	-	-	1/2" TREATED	SEE RMKS	-	DN CHASE FROM REVERSE OSMOSIS SYSTEM. BEV INSTALLER TO CONN CW LINE, PER LOCAL CODES
1	8025.02 P2	RELOCATED ICED TEA BREWER	-	-	-	-	-	1/2" TREATED	SEE RMKS	-	DN CHASE FROM SODA SYSTEM. BEV INSTALLER TO CONN CW LINE, PER LOCAL CODES
1	8028.13 P2	RELOCATED SODA TOWER	-	-	-	-	-	6" PVC CONDUIT	SEE RMKS	-	ABOVE CEILING FROM SODA SYSTEM - TERMINATE AT CHASE
1	8028.13 P3	RELOCATED SODA TOWER	-	-	-	-	-	6" DRINK COND.	SEE RMKS	-	DN CHASE FROM SODA SYSTEM - BSI TO MAKE FINAL CONNECTIONS, PER LOCAL CODES
2	8039.22 P2	RELOCATED ICE MACHINE	-	-	-	-	-	1/2" TREATED	-	-	FLEX LINE OVERHEAD FROM SODA SYSTEM - BSI TO MAKE FINAL CONNECTIONS, PER LOCAL CODES
2	8039.22 P3	RELOCATED ICE MACHINE	-	-	-	-	-	REFRIG LINES	-	-	PRE-CHARGED REFRIGERATION LINES OVERHEAD FROM REMOTE CONDENSING UNIT
1	8205.10 P1	RELOCATED FROZEN CARBONATED BEVERAGE (FCB)	-	-	-	-	-	-	-	-	PC TO RELOCATE UTILITIES AS NEEDED
2	8700.10 P1	RELOCATED BULK OIL SYSTEM	-	-	-	-	-	SEE RMKS	-	-	PC TO RELOCATE UTILITIES AS NEEDED

REV	DATE	DESCRIPTION	BY

ENGINEER OF RECORD:

STATE OF MISSOURI
JOHN DALE FERGUSON
PROFESSIONAL ENGINEER
4/12/19

PREPARED BY:
CORE STATES
GROUP
CORESTATES, INC.
1700 Industrial Drive
Suite B
Rogers, AR 72756
479.986.4400
www.core-eng.com

PREPARED FOR:
McDonald's USA, LLC

©2019 McDonald's Corporation

These drawings and specifications are the confidential and proprietary property of McDonald's USA, LLC and shall not be copied or reproduced without written authorization. The contract documents were prepared for use on this specific site in conjunction with its issue date and are not suitable for use on a different site or at a later time. Use of these drawings for reference or example on another project requires the services of properly licensed architects and engineers. Reproduction of the contract documents for reuse on another project is not authorized.

DRAWN BY
CHR
STD ISSUE DATE
MAY 2018
REVIEWED BY
J.FERGUSON
DATE ISSUED
10/12/18
C.S.G. PROJECT #
MCD-24772

TITLE
MRP PROGRAM
CORE 16 2.0

DESCRIPTION
EXISTING MASONRY WALL CONSTRUCTION
EXISTING WOOD ROOF TRUSSES
TILE ARCADES - FRONT, ENTRY

SITE ID
024-0294
SITE ADDRESS
815 EASTLAND DRIVE
JEFFERSON CITY, MO 65101

SHEET NO.
K3.0
SCHEDULES

ELECTRICAL SCHEDULE

Count	ITEM #	ITEM DESCRIPTION	VOLT PHASE	FLA DRAW	HP	RECEP TYPE	BRKR SIZE	COND WS	PNL CKT	HGT AFF	REQUIREMENTS
1	130.00 E3	COMBI-BLODGETT OVEN	208/3	20.0	-	L4-30R9	30A	1/2"C-3#10	DETERMINE IN FIELD	SEE RMKS	PLUGS INTO CHASE RECEPT#HBL320R6W PROVIDED BY KES, AND MAKE FINAL CONNECTIONS
1	141.10 E3	HOUDINI- OVEN VENTLESS HOOD	120/1	8.0	-	5-20R	15A	1/2"C-2#12	DETERMINE IN FIELD	SEE RMKS	UNIT PLUGES INTO CHASE . EC MAKE FINAL CONNECTIONS
1	171.07 E1	WALK-IN COOLER / FREEZER WITH FLOORS	120/1	10.00	-	JB	20A	1/2"C-2#12 EA	DETERMINE IN FIELD	@ CLG	JB FOR LIGHTS &]DOOR HEATER- UNSWITCHED LIGHT TO BE IN BOTH COOLER & FREEZER,EC TO CONNECT POWER
1	171.07 E2	WALK-IN COOLER / FREEZER WITH FLOORS	-	-	-	-	-	-	-	VIF	EC TO FURNISH & INSTALL CONDUIT,WIRE & LIGHT FIXTURES& OTHER DEVICES INSIDE COOLER/FREEZER BOX
1	174.00 E1	REMOTE CONDENSING UNIT	208-230/3	41.0	1.5(C) 3	JB	50A	1"C-3#6	DETERMINE IN FIELD	VIF	TERMINATE POWER CONDUCTORS TO REMOTE CONDENSING UNIT FUSABLE DISCONNECT SWITCH
1	174.00 E2	REMOTE CONDENSING UNIT	LOW VOLT WIRES	-	-	-	-	-	-	VIF	L V WIRES CONNECT MAC UNIT TO EVAPS & SHALL BE ROUTED IN SEALTITE WHERE EXPOSED TO WEATHER
1	175.08 E1	COOLER EVAPORATOR - AIR-COOLED	208-230/1	-	-	JB	20A SEE RMKS	1/2"C-2#12	PWR BY MAC UNIT	VIF	ELIMINATE CIRCUIT BREAKER IF USED WITH MAC UNIT
1	175.08 E2	COOLER EVAPORATOR - AIR-COOLED	LOW VOLT WIRES	-	-	-	-	-	-	@ CLG	L V WIRES CONN MAC UNIT TO EVAPS & SHALL BE ROUTED SEPARATELY FROM POWER CONDUCTORS
1	176.21 E1	FREEZER EVAPORATOR - AIR-COOLED	208-230/1	-	-	JB	30A SEE RMKS	1/2"C-2#10	PWR BY MAC UNIT (SEE NOTE 11)	@ CLG	NO CCT BREAKER REQ WITH MAC UNIT-IF FAN SHUT-OFF SW. REQ SYS PUMPDOWN RELAY MUST BE INSTALLED
1	176.21 E2	FREEZER EVAPORATOR - AIR-COOLED	LOW VOLT WIRES	-	-	-	-	-	-	@ CLG	L V WIRES CONN MAC UNIT TO EVAPS & SHALL BE ROUTED SEPARATELY FROM POWER CONDUCTORS
1	179.11 E1	COUNTER TOP DISPLAY CASE - 22" WIDE	120/1	2.5	0	5-20R	20A	1/2"C-2#12	DETERMINE IN FIELD	1'-6"	EC TO BRING POWER DOWN WALL, PROVIDE/INSTALL RECEPTACLE
1	179.11 E2	COUNTER TOP DISPLAY CASE - 22" WIDE	120/1	2.5	0	5-20R	20A	1/2"C-2#12	DETERMINE IN FIELD	SEE RMKS	PROVIDE IG RECEP. IN COUNTER- MOUNTED RACEWAY
1	181.04 E1	REFRIGERATOR - WORK TOP - 48" WIDE	120/1	4.5	1/5	5-20R	20A	1/2"C-2#12	DETERMINE IN FIELD	2'-0"	EC TO BRING POWER DOWN WALL, PROVIDE/INSTALL RECEPTACLE
1	207.09 E1	30" BASE REFRIGERATOR	120/1	3.2	-	5-20R	20A	1/2"C-2#12	DETERMINE IN FIELD	2'-0"	EC TO BRING POWER DOWN WALL, PROVIDE/INSTALL RECEPTACLE
1	207.09 E3	30" BASE REFRIGERATOR	120/1	3.2	-	5-20R	20A	1/2"C-2#12	DETERMINE IN FIELD	SEE RMKS	PLUGS TO EQUIPMENT MOUNTED BREAKER PANEL OR OUTLET BOX, EC MAKE FINAL CONNECTIONS
1	207.10 E1	FINISHING STATION	120/1	8.0	-	5-20R	20A	1/2"C-2#12	DETERMINE IN FIELD	2'-0"	EC TO BRING POWER DOWN WALL, PROVIDE/INSTALL RECEPTACLE
2	21.01 E3	COFFEE BREWER	208/1	15	-	L14-20R	20A SEE RMKS	1/2"C-3#12	DETERMINE IN FIELD	2'-3"	EC TO BRING POWER DOWN WALL, PROVIDE/INSTALL RECEPTACLE
1	213.00 E1	TABLE LOCATOR SYSTEM	120/1 ISOLATED	1.5	-	-	20A	1/2"C-2#12IG	CP:4	SEE RMKS	POWER FROM SAME RECEP. AS DELIVERY TABLE IN COUNTER-MOUNTED RACEWAY
1	215.00 E10	POS REGISTER - FRONT COUNTER	DATA CABLE	-	-	4x4x4 PB	-	-	DETERMINE IN FIELD	1'-2"	EXTEND 2 1/2" CONDUIT TO 215.11 FOR POS DATA CABLES
1	215.00 E6	POS REGISTER - FRONT COUNTER	DATA CABLE	-	-	4x4x4 PB	-	-	DETERMINE IN FIELD	1'-2"	EXTEND 2 1/2" CONDUIT UNDER SLAB
1	215.17 E1	DELIVERY TABLET	120/1 ISOLATED	1.5	-	IG5262	20A	1/2"C-2#12IG	-	SEE RMKS	GC TO PROVIDE IG RECEP. IN COUNTER MOUNTED RACEWAY
1	216.04 E3	ORB MONITOR (MINI)	120/1 ISOLATED	1.5 EA.	-	IG5262	20A	3/4"C-2#12IG	DETERMINE IN FIELD	SEE RMKS	PROVIDE IG RECEP. IN COUNTER- MOUNTED RACEWAY
1	217.00 E1	PARK/ROTATE/SERVE BUMP BAR	DATA CABLE	-	-	-	-	-	EXISTING/RELOCATED	SEE RMKS	POS TO COORD W/ MCD O/O, RELOCATE EXIST. AS REQUIRED.
1	219.00 E7	POS - RECEIPT PRINTER	120/1 ISOLATED	0.7	-	IG4710	20A	1/2"C-2#12IG	DETERMINE IN FIELD	SEE RMKS	PLUGS INTO CHASE OR SURFACE MOUNT RECEPTACLE IG4710
1	219.00 E8	POS - RECEIPT PRINTER	DATA CABLE	-	-	-	-	-	-	SEE RMKS	CABLE FURNISHED AND INSTALLED BY POS SYSTEM SUPPLIER
1	23.05 E3	CREAM DISPENSER	120/1	4.0	-	5-20R	20A SEE RMKS	1/2"C-2#12	-	2'-3"	EC TO BRING POWER DOWN WALL, PROVIDE/INSTALL RECEPTACLE
1	24.01 E4	ORANGE JUICE DISPENSER, DUAL FLAVOR	120/1	10.0	-	5-20R	20A SEE RMKS	1/2"C-2#12	SEE RMKS	2'-3"	EC TO BRING POWER DOWN WALL, PROVIDE/INSTALL RECEPTACLE
1	44.29 E1	BREAKER PANEL- 125 AMP - 3 PHASE EQUIPMENT MOUNTED	120-208/3	SEE RMKS	-	-	125A	2"C-4#1	DETERMINE IN FIELD	SEE RMKS	EC TO EXTEND EXISTING SERVICE AS REQ & CONNECT TO PANEL
1	44.30 E1	BREAKER PANEL- 125 AMP - 1 PHASE EQUIPMENT MOUNTED	120-208/1	SEE RMKS	-	-	125A	2"C-4#1	DETERMINE IN FIELD	SEE RMKS	EC TO EXTEND EXISTING SERVICE AS REQ & CONNECT TO PANEL
1	73.00 E1	UNIVERSAL EXHAUST HOOD (R.H.) ELECTRIC 3-VAT FRYER	120/1	12.5, 9.8	-	-	20A	1/2"C-2#12	DETERMINE IN FIELD	SEE RMKS	EC TO CONN POWER TO RACEWAY FLA = 12.0 FRYER CONTROLS, 0.5 CAPTURE JET & 9.8 INDIVID. EXHAUST FAN INTERLOCK
1	8020.00 E1	RELOCATED AUTOMATED BEVERAGE SYSTEM	VERIFY	VERIFY DRAW	VERIFY	VERIFY	VERIFY BREAKER	VERIFY	DETERMINE IN FIELD	SEE RMKS	EC TO BRING POWER DOWN CHASE AND CONNECT TO CHASE MOUNTED RECEPTACLE
1	8020.00 E2	RELOCATED AUTOMATED BEVERAGE SYSTEM	VERIFY	VERIFY DRAW	VERIFY	VERIFY	VERIFY BREAKER	VERIFY	DETERMINE IN FIELD	SEE RMKS	EC TO BRING POWER DOWN WALL, PROVIDE/INSTALL RECEPTACLE
1	8020.00 E3	RELOCATED AUTOMATED BEVERAGE SYSTEM	VERIFY	-	-	-	-	VERIFY	DETERMINE IN FIELD	SEE RMKS	CABLE FURNISHED/INSTALLED BY POS INSTALLER
2	8021.01 E1	RELOCATED COFFEE BREWER	VERIFY	VERIFY DRAW	VERIFY	VERIFY	20A SEE RMKS	VERIFY	DETERMINE IN FIELD	SEE RMKS	PLUGS TO EQUIPMENT MOUNTED BREAKER PANEL OR OUTLET BOX, EC MAKE FINAL CONNECTIONS
1	8021.10 E2	RELOCATED SPECIALTY COFFEE	VERIFY	VERIFY DRAW	VERIFY	VERIFY	30A SEE RMKS	VERIFY	DETERMINE IN FIELD	SEE RMKS	EC TO BRING POWER DOWN CHASE AND CONNECT TO CHASE MOUNTED RECEPTACLE
1	8021.11 E2	RELOCATED SMOOTHIE MACHINE	VERIFY	VERIFY DRAW	VERIFY	VERIFY	20A SEE RMKS	VERIFY	DETERMINE IN FIELD	SEE RMKS	EC TO BRING POWER DOWN CHASE AND CONNECT TO CHASE MOUNTED RECEPTACLE
1	8023.05 E1	RELOCATED CREAM DISPENSER	VERIFY	VERIFY DRAW	VERIFY	VERIFY	VERIFY BREAKER	VERIFY	DETERMINE IN FIELD	SEE RMKS	PLUGS TO EQUIPMENT MOUNTED BREAKER PANEL OR OUTLET BOX, EC MAKE FINAL CONNECTIONS
1	8024.01 E3	RELOCATED ORANGE JUICE DISPENSER, DUAL FLAVOR	VERIFY	VERIFY DRAW	VERIFY	VERIFY	VERIFY BREAKER	VERIFY	DETERMINE IN FIELD	SEE RMKS	PLUGS TO EQUIPMENT MOUNTED BREAKER PANEL OR OUTLET BOX, EC MAKE FINAL CONNECTIONS
1	8025.02 E2	RELOCATED ICED TEA BREWER	VERIFY	VERIFY DRAW	VERIFY	VERIFY	VERIFY BREAKER	VERIFY	DETERMINE IN FIELD	SEE RMKS	EC TO INSTALL/RELOCATE POWER/RECEPTACLES, BRING DOWN CHASE. EC TO MAKE FINAL CONNECTS
1	8028.13 E1	RELOCATED SODA TOWER	VERIFY	VERIFY DRAW	VERIFY	VERIFY	VERIFY BREAKER	VERIFY	DETERMINE IN FIELD	SEE ELEV	EC TO BRING POWER DOWN WALL, PROVIDE/INSTALL RECEPTACLE
2	8039.22 E3	RELOCATED ICE MACHINE	VERIFY	VERIFY DRAW	VERIFY	VERIFY	VERIFY BREAKER	VERIFY	DETERMINE IN FIELD	@ CLG	CIRCUIT BREAKERS SHALL BE HACR TYPE
2	8043.15 E1	RELOCATED HEATED LANDING ZONE	VERIFY	VERIFY DRAW	VERIFY	VERIFY	VERIFY BREAKER	VERIFY	DETERMINE IN FIELD	SEE RMKS	PLUGS INTO CENTER ISLAND BREAKER PANEL OR OUTLET HOUSING
1	8065.29 E1	RELOCATED 3-VAT FRYER - ELECTRIC - S/S/S	VERIFY	VERIFY DRAW	VERIFY	VERIFY	VERIFY BREAKER	VERIFY	DETERMINE IN FIELD	SEE RMKS	PLUGS INTO RACEWAY RECEP WITH(1)L21-20P INTERLOCK PLUG &(3) 15-60P POWER PLUG BY KES
1	8096.11 E1	RELOCATED 36" CLAMSHELL GRILL - 3 PLATEN - ELECTRIC	VERIFY	VERIFY DRAW	VERIFY	VERIFY	VERIFY BREAKER	VERIFY	DETERMINE IN FIELD	-	PLUGS IN RACEWAY RECEP WITH(1)L21-20P INTERLOCK & (2) 15-50P POWER PLUG EA GRILL BY KES
1	8096.15 E1	RELOCATED 36" CLAMSHELL GRILL - 2 PLATEN - ELECTRIC	VERIFY	VERIFY DRAW	VERIFY	VERIFY	VERIFY BREAKER	VERIFY	DETERMINE IN FIELD	-	PLUGS IN RACEWAY RECEP WITH(1)L21-20P INTERLOCK & (2) 15-50P POWER PLUG EA GRILL BY KES
1	8097.07 E2	RELOCATED GRILL SIDE MEAT FREEZER - DOUBLE WIDE	VERIFY	VERIFY DRAW	VERIFY	VERIFY	VERIFY BREAKER	VERIFY	DETERMINE IN FIELD	SEE RMKS	UNIT PLUGS INTO CHASE RECEPTACLE
2	8116.01 E1	RELOCATED UNIVERSAL HOLDING CABINET - 2-SIDED - PIN & SLEEVE	VERIFY	VERIFY DRAW	VERIFY	VERIFY	VERIFY BREAKER	VERIFY	DETERMINE IN FIELD	SEE RMKS	PLUGS INTO OVERHEAD RECEPTACLE # 330C6W(B) PROVIDED BY KES- HEIGHT TO BOTTOM OF RECEPTACLE
1	8116.23 E1	RELOCATED UNIVERSAL HOLDING CABINET - HD -2-SIDED - P&S	VERIFY	VERIFY DRAW	VERIFY	VERIFY	VERIFY BREAKER	VERIFY	DETERMINE IN FIELD	SEE RMKS	PLUGS INTO OVERHEAD RECEPTACLE # 330C6W(B) PROVIDED BY KES- HEIGHT TO BOTTOM OF RECEPTACLE
2	8117.13 E1	RELOCATED UHC TABLE - 2 SIDED	VERIFY	VERIFY DRAW	VERIFY	VERIFY	VERIFY BREAKER	VERIFY	DETERMINE IN FIELD	SEE RMKS	PLUGS INTO OVERHEAD RECEPTACLE - HEIGHT OT BOTTOM OF RECEPTACLE
2	8118.00 E1	RELOCATED Q'ING OVEN - PIN & SLEEVE	VERIFY	VERIFY DRAW	VERIFY	VERIFY	VERIFY BREAKER	VERIFY	DETERMINE IN FIELD	SEE RMKS	PLUGS INTO OVERHEAD RECEPTACLE # 320C6W(B) PROVIDED BY KES- HEIGHT OT BOTTOM OF RECEPTACLE
1	8118.00 E6	RELOCATED Q'ING OVEN - PIN & SLEEVE	VERIFY	VERIFY DRAW	VERIFY	VERIFY	VERIFY BREAKER	VERIFY	DETERMINE IN FIELD	SEE ELEV	UNIT PLUGS INTO CHASE RECEPTACLE
1	8121.00 E1	RELOCATED MUFFIN TOASTER PIN & SLEEVE	VERIFY	VERIFY DRAW	VERIFY	VERIFY	VERIFY BREAKER	VERIFY	DETERMINE IN FIELD	SEE RMKS	GC TO RELOCATE OR INSTALL NEW UTILITIES AS REQ. FOR RELOCATED EQP. INTO OEP
1	8122.22 E1	RELOCATED UNIVERSAL TOASTER - P&S	VERIFY	VERIFY DRAW	VERIFY	VERIFY	VERIFY BREAKER	VERIFY	DETERMINE IN FIELD	SEE RMKS	PLUGS INTO OVERHEAD RECEPTACLE # 330C6W(B) PROVIDED BY KES -HEIGHT TO BOTTOM OF RECEPTACLE
1	8122.23 E1	RELOCATED CLUB TOASTER - P&S	VERIFY	VERIFY DRAW	VERIFY	VERIFY	VERIFY BREAKER	VERIFY	DETERMINE IN FIELD	SEE RMKS	PLUGS INTO OVERHEAD RECEPTACLE # 330C6W(B) PROVIDED BY KES -HEIGHT TO BOTTOM OF RECEPTACLE
1	8123.24 E1	RELOCATED PREP TABLE (2 SIDED) 34" X 75" - PIN & SLEEVE	VERIFY	VERIFY DRAW	VERIFY	VERIFY	VERIFY BREAKER	VERIFY	DETERMINE IN FIELD	SEE RMKS	PLUGS INTO OVERHEAD RECEPTACLE # 330C6W(B) PROVIDED BY KES- HEIGHT TO BOTTOM OF RECEPTACLE
1	8131.02 E5	RELOCATED BISCUIT OVEN	VERIFY	VERIFY DRAW	VERIFY	VERIFY	VERIFY BREAKER	VERIFY	DETERMINE IN FIELD	SEE RMKS	UNIT PLUGS INTO CHASE RECEPTACLE
1	8143.00 E3	RELOCATED EGG COOKER	VERIFY	VERIFY DRAW	VERIFY	VERIFY	VERIFY BREAKER	VERIFY	DETERMINE IN FIELD	SEE RMKS	PLUGS INTO OVERHEAD RECEPT PROVIDED BY KES - HT TO BOTTOM OF RECEPT
1	8177.00 E1	RELOCATED REACH-IN REFRIGERATOR-SINGLE WIDE	VERIFY	VERIFY DRAW	VERIFY	VERIFY	VERIFY BREAKER	VERIFY	DETERMINE IN FIELD	SEE RMKS	EC TO BRING POWER DOWN WALL, PROVIDE/INSTALL RECEPTACLE
1	8177.00 E2	RELOCATED REACH-IN REFRIGERATOR-SINGLE WIDE	VERIFY	VERIFY DRAW	VERIFY	VERIFY	VERIFY BREAKER	VERIFY	DETERMINE IN FIELD	SEE RMKS	EC TO BRING POWER DOWN CHASE AND CONNECT TO CHASE MOUNTED RECEPTACLE
1	8179.01 E1	RELOCATED REFRIGERATOR - PASS-THRU	VERIFY	VERIFY DRAW	VERIFY	VERIFY	VERIFY BREAKER	VERIFY	DETERMINE IN FIELD	SEE RMKS	PLUGS INTO OVERHEAD RECEPT #320C4W(Y) PROVIDED BY KES - HT TO BOTTOM OF RECEPT
1	8181.01 E2	RELOCATED REFRIGERATOR- SPECIALTY COFFEE - 27" WIDE	VERIFY	VERIFY DRAW	VERIFY	VERIFY	VERIFY BREAKER	VERIFY	DETERMINE IN FIELD	SEE RMKS	EC TO BRING POWER DOWN CHASE AND CONNECT TO CHASE MOUNTED RECEPTACLE
1	8203.02 E2	RELOCATED HEAT TREAT COMBINATION SHAKE/SUNDAE MACHINE	VERIFY	VERIFY DRAW	VERIFY	VERIFY	VERIFY BREAKER	VERIFY	DETERMINE IN FIELD	SEE RMKS	EC TO BRING POWER DOWN CHASE AND CONNECT TO CHASE MOUNTED RECEPTACLE
1	8205.10 E2	RELOCAED FROZEN CARBONATED BEVERAGE (FCB)	VERIFY	VERIFY DRAW	VERIFY	VERIFY	VERIFY BREAKER	VERIFY	DETERMINE IN FIELD	SEE RMKS	PLUGS TO EQUIPMENT MOUNTED BREAKER PANEL OR OUTLET BOX, EC MAKE FINAL CONNECTIONS
2	8207.09 E1	RELOCATED BASE REFRIGERATOR	VERIFY	VERIFY DRAW	VERIFY	VERIFY	VERIFY BREAKER	VERIFY	DETERMINE IN FIELD	SEE RMKS	EC TO BRING POWER DOWN WALL, PROVIDE/INSTALL RECEPTACLE
2	8215.00 E12	RELOCATED POS REGISTER - FRONT CONTER	VERIFY	VERIFY DRAW	VERIFY	VERIFY	VERIFY BREAKER	VERIFY	DETERMINE IN FIELD	SEE RMKS	PROVIDE IG RECEP. IN COUNTER- MOUNTED RACEWAY
2	8215.98 E1	RELOCATED POS PC HARDWARE - 2 BOOTH D/T	VERIFY	VERIFY DRAW	VERIFY	VERIFY	VERIFY BREAKER	VERIFY	DETERMINE IN FIELD	SEE RMKS	EC TO RELO ELEC AS REQ. COORDINATE LOCATION W/ O/O, POS INSTALLER TO CONNECT
2	8215.98 E2	RELOCATED POS PC HARDWARE - 2 BOOTH D/T	VERIFY	VERIFY DRAW	VERIFY	VERIFY	VERIFY BREAKER	VERIFY	DETERMINE IN FIELD	SEE RMKS	CABLE FURNISHED/INSTALLED/RELOCATED BY POS INSTALLER
1	8216.00 E1	RELOCATED POS - VIDEO MONITOR	VERIFY	VERIFY DRAW	VERIFY	VERIFY	VERIFY BREAKER	VERIFY	DETERMINE IN FIELD	SEE ELEV	EC TO PROVIDE/INSTALL RECEPTACLE, POS INSTALLER TO CONNECT POS
9	8216.00 E2	RELOCATED POS - VIDEO MONITOR	VERIFY	VERIFY DRAW	VERIFY	VERIFY	VERIFY BREAKER	VERIFY	DETERMINE IN FIELD		CABLE FURNISHED/INSTALLED BY POS INSTALLER
3	8216.00 E3	RELOCATED POS - VIDEO MONITOR	VERIFY	VERIFY DRAW	VERIFY	VERIFY	VERIFY BREAKER	VERIFY	DETERMINE IN FIELD	SEE RMKS	CABLE FURNISHED AND INSTALLER BY POS SUPPLIER
5	8216.00 E7	RELOCATED POS - VIDEO MONITOR @ CHASE	VERIFY	VERIFY DRAW	VERIFY	VERIFY	VERIFY BREAKER	VERIFY	DETERMINE IN FIELD	SEE RMKS	EC TO BRING POWER DOWN CHASE AND CONNECT TO CHASE MOUNTED RECEPTACLE
1	8216.05 E2	RELOCATED ORB MONITOR	VERIFY	VERIFY DRAW	VERIFY	VERIFY	VERIFY BREAKER	VERIFY	DETERMINE IN FIELD	SEE ELEV	BRING POWER DOWN WALL, CABLE FURNISHED AND INSTALLER BY POS SUPPLIER
3	8218.00 E1	RELOCATED POS - CASH DRAWER	VERIFY	VERIFY DRAW	VERIFY	VERIFY	VERIFY BREAKER	VERIFY	DETERMINE IN FIELD	SEE RMKS	POWER FROM SAME ELECT. PNL. AND SAME PHASE AS OTHER POS
2	8219.00 E10	RELOCATED POS - RECEIPT PRINTER	VERIFY	VERIFY DRAW	VERIFY	VERIFY	VERIFY BREAKER	VERIFY	DETERMINE IN FIELD	SEE RMKS	PROVIDE IG RECEP. IN COUNTER- MOUNTED RACEWAY
1	8219.00 E7	POS - RECEIPT PRINTER	VERIFY	VERIFY DRAW	VERIFY	VERIFY	VERIFY BREAKER	VERIFY	DETERMINE IN FIELD	SEE RMKS	PLUGS INTO CHASE OR SURFACE MOUNT RECEPTACLE IG4710
1	8219.00 E8	POS - RECEIPT PRINTER	VERIFY	VERIFY DRAW	VERIFY	VERIFY	VERIFY BREAKER	VERIFY	-	SEE RMKS	CABLE FURNISHED AND INSTALLED BY POS SYSTEM SUPPLIER
1	8237.00 E1	RELOCATED PIE DISPLAY	VERIFY	VERIFY DRAW	VERIFY	VERIFY	VERIFY BREAKER	VERIFY	DETERMINE IN FIELD	SEE ELEV	OPTIONAL LOCATION - VERIFY HEIGHT W/PROJECT MANAGER
5	8700.09 E1	RELOCATED ECONOMY OEP BOX W/MOUNTING HARDWARE	VERIFY	-	-	-	-	-	DETERMINE IN FIELD	SEE RMKS	CEILING MOUNTED
2	8700.10 E1	RELOCATED BULK OIL SYSTEM	VERIFY	VERIFY DRAW	VERIFY	VERIFY	VERIFY BREAKER	-	DETERMINE IN FIELD	SEE RMKS	EC TO RELOCATE UTILITIES AS REQUIRED
1	9.14 E1	UTILITY CHASE-D/T BEVERAGE VERSION	SEE RMKS	-	-	-	-	-	-	SEE RMKS	CHASE AND RECEPTACLES BY KES, EC TO RUN WIRES AND MAKE FINAL CONNECTIONS
1	90.80 E1	CAPTURE JET FOR 3 VAT FRYER	120/1	0.72	-	-	20A	1/2"C-2#12	DETERMINE IN FIELD	SEE RMKS	EC TO EXTEND CONDUIT/CONDUCTORS DN CHASE TO TEMINAL BLOCK, MAKE FINAL CONNECTIONS (SEE SPECIFICATIONS)
1	90.83 E1	CAPTURE JET FOR 83" HOOD (2)GRILLS	120/1	0.72	-	-	20A	1/2"C-2#12	DETERMINE IN FIELD	SEE RMKS	EC TO EXTEND CONDUIT/CONDUCTORS DN CHASE TO TEMINAL BLOCK, MAKE FINAL CONNECTIONS (SEE SPECIFICATIONS)
1	91.00 E1	WALL MOUNT FREEZER-SINGLE WIDE- HIGH CAPACITY	120/1	5.0	-	5-20R	20A	1/2"C-2#12	DETERMINE IN FIELD	SEE ELEV	EC TO BRING POWER DOWN WALL, PROVIDE/INSTALL RECEPTACLE
1	94.06 E1	UNIVERSAL EXHAUST HOOD (L.H.) 2-ELEC FULL-CLAM GRILLS	120/1	13.3	-	-	20A	1/2"C-2#12	DETERMINE IN FIELD	SEE RMKS	EC TO CONN. POWER TO RACEWAY FLA = (2) 3.7 GRILL CONTROLS & 5.9 INDIVID. EXHAUST FAN INTERLOCK

REV	DATE	DESCRIPTION	BY

ENGINEER OF RECORD:

JOHN DALE FERGUSON

4/12/19

PREPARED BY:

CORE STATES
GROUP
CORESTATES, INC.

1700 Industrial Drive
Suite B
Rogers, AR 72756
479.986.4400
www.core-eng.com

PREPARED FOR:

McDonald's USA, LLC

These drawings and specifications are the confidential and proprietary property of McDonald's USA, LLC and shall not be copied or reproduced without written authorization. The contract documents were prepared for use on this specific site in conjunction with its issue date and are not suitable for use on a different site or at a later time. Use of these drawings for reference or example on another project requires the services of properly licensed architects and engineers. Reproduction of the contract documents for reuse on another project is not authorized.

DRAWN BY
CHR

STD ISSUE DATE
MAY 2018

REVIEWED BY
J.FERGUSON

DATE ISSUED
10/12/18

C.S.G. PROJECT #
MCD-24772

TITLE
MRP PROGRAM
CORE 16 2.0

DESCRIPTION
EXISTING MASONRY WALL CONSTRUCTION
EXISTING WOOD ROOF TRUSSES
TILE ARCADES - FRONT, ENTRY

SITE ID
024-0294

SITE ADDRESS
815 EASTLAND DRIVE JEFFERSON CITY, MO 65101

SHEET NO.
K4.0
ELECTRICAL SCHEDULE